



0.001

EXT-01240
11/02/2026 | MA3-Quadrado

	Limite do terreno - Lote 1
	Alinhamentos fornecidos pelo município
	Área de Implantação / Impermeabilização - Cimp, 1
	Limite Área Agrícola
	Parte Restante
	Área Ajudinada - Cimp, 0
	Área Exterior Pavimentada - Cimp, 0,50
	Pavimento em microcubo
	Construções vizinhas
	Zona ajudinada

DADOS DA OPERAÇÃO URBANÍSTICA	
DESIGNAÇÃO	ÁREA (m ²)
00. Área Total - Lote 1	1 800,00
01. Área de Implantação / Impermeabilização - Cimp. 1	431,60
02. Área Bruta de Construção	1 709,20
03. Área de Estacionamento	363,29
04. Área Exterior Pavimentada - Cimp. 0.5	587,05
05. Área Agradinada - Cimp. 0	749,74
06. Área Útil	922,10
07. Área Habitável	699,54

projeto	projetos
Edifício de Habitação Multi-Familiar	
Obra de Edificação	
local	Rua da Extrema - Lapa
2008-16	São Carlos, Portugal
responsável	UMBAU - Imobiliária e Construção Lda
referência	EXT
tema	Comunicação Privada
data	agosto 2008
autor	José Pedro Paulo DA
núcleo da desenh	desenho de arquitetura
escala	1:2000
desenho	Desenhos Gerais
Planta de Implantação sobre	
Levantamento Topográfico	
resumo	R01
nota	

1.01.001


ESTE DESENHO É PROPRIEDADE INTELECTUAL DA GCPA PORTUGAL. - SUPLENIMENTOS INDEBIDAMENTE À SUA REPRODUÇÃO TOTAL OU PARCIAL, NÃO É PERMITIDA. A REPRODUÇÃO DESTE PROJETO OU DE QUALQUER PARTE DO MESMO, SEM A AUTORIZAÇÃO DA GCPA PORTUGAL, É PROIBIDA. A GCPA PORTUGAL NÃO SE RESPONSABILIZA POR ERROS OU OMISSÕES QUE SE ENCONTREM NESTE PROJETO. A GCPA PORTUGAL NÃO SE RESPONSABILIZA POR ERROS OU OMISSÕES QUE SE ENCONTREM NESTE PROJETO.

Área reservada ao município

LEGENDA

- Limite do terreno - Lote 1
- Área de Implantação
- Pavimento em microcubo
- Percurso pedonal

DADOS DA OPERAÇÃO URBANÍSTICA	
DESIGNAÇÃO	ÁREA (m2)
00. Área Total - Lote 1	1 800,00
01. Área de Implantação / Impermeabilização - Cimp. 1	431,60
02. Área Bruta de Construção	1 709,20
03. Área de Estacionamento	383,29
04. Área Exterior Pavimentada - Cimp. 0.5	587,05
05. Área Ajardinada - Cimp. 0	749,74
06. Área Util	922,10
07. Área Habitável	699,54

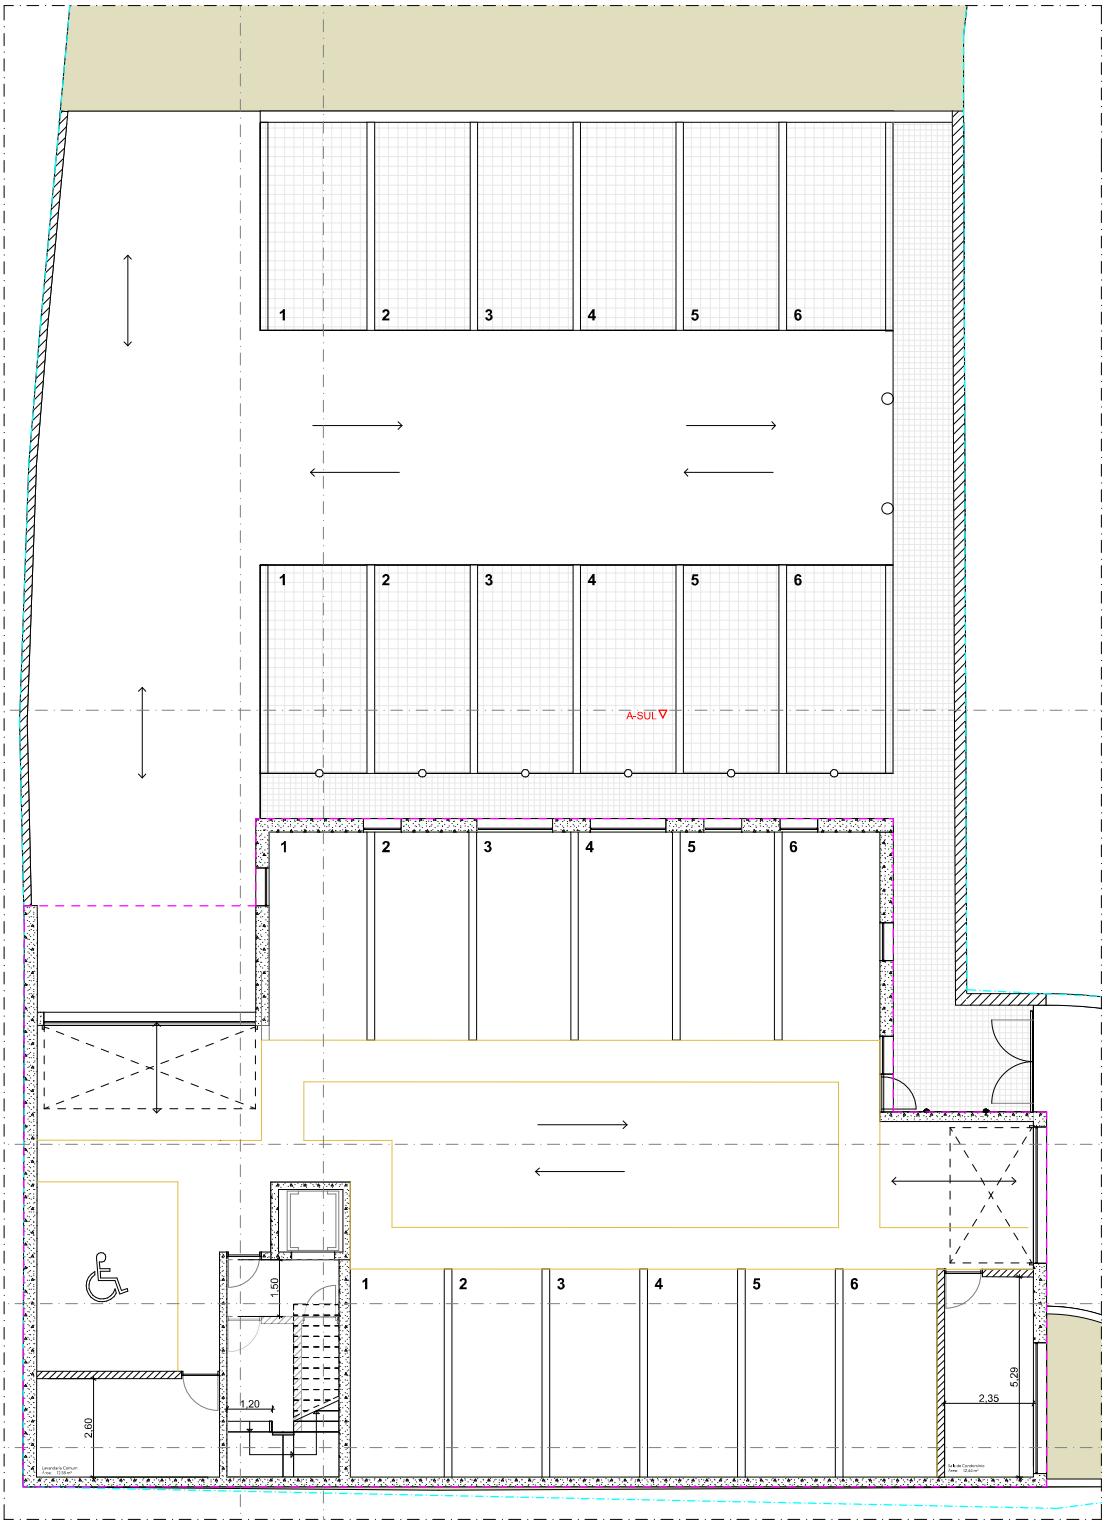

projeto
arquiteto
Edifício de Habitação Multi-Família
Cidade do Fátima
Rua da Estrela - Lote 1
Sítio Casimiro, Portugal
registo
LHBAU - Imobiliária e
Condições URB
referência
EXT
tela
Comunicação Privada
data
agosto 2025
autor
Jorge F. Fernandes, Inc.
estudo
DA 2025
escala
1:100
desenho
Desenho Geral
título
Planta Piso Cave
R01

1.01.002



DADOS DA OPERAÇÃO URBANÍSTICA		ÁREA (m2)
00.	Área Total - Lote 1	1 800,00
01.	Área de Implantação / Impedimentalização - Cimp. 1	431,60
02.	Área Bruta de Construção	1 709,20
03.	Área de Estacionamento	383,29
04.	Área Exterior Pavimentada - Cimp. 0,5	987,05
05.	Área Alargada - Cimp. 0	748,74
06.	Área Utiil	922,10
07.	Área Habitável	699,54

projeto	Edifício de Habitação Multifamiliar
local	Obra de Educação Infantil
location	Rua da Estrela - Lote 10 - São Cosme, Portugal
requerente	São Cosme, Portugal
edificício	UMBAU - instalação da Construção de
referência	2017
phase	Comunicação Privada
date	agosto 2017
autor	Júlio Pedroso
data do desenho	04 dezembro
scale	1:100
desenho	Desenhos Gerais
revisão	Planta Rés do Chão
data no	R017
scale no	1.01.003

ASUL V

ANORA

LEGENDA

Limite das frações

Linhas em vista

DADOS DA OPERAÇÃO URBANÍSTICA	
DESIGNAÇÃO	ÁREA (m2)
00. Área Total - Lote 1	1 800.00
01. Área de Implantação / Impermeabilização - Cimp. 1	431.60
02. Área Bruta de Construção	1 705.20
03. Área de Estacionamento	383.29
04. Área Exterior Pavimentada - Cimp. 0.5	587.05
05. Área Alagadada - Cimp. 0	749.74
06. Área Util	922.10
07. Área Habitável	699.54

projeto
project

Edifício de Habitação Multifamiliar

Obra de Edificação

local

location

Rua da Extrema - Lote 1

responsável técnico

technical responsible

Soc Cosme Portugal

referência

reference

UMBAU - Imobiliária e Construção Lda

fase

phase

Comunicação Prévia

data

date

agosto 2026

autor

author

João Filipe de Sousa

autor de desenhos

drawings author

DA 08504

escala

scale

1:100

desenho

drawing

Desenho Geral

revisão

revision

Planta Pisc. 1

autor

author

R01

1.01.004



A-SUL ▽


LEGENDA

	Limite das frações
	Linhas em vista


DADOS DA OPERAÇÃO URBANÍSTICA		ÁREA (m2)
DESIGNAÇÃO		
00. Área Total - Lote 1		1 800,00
01. Área de Implantação / Impemobilização - Cimp. 1		431,60
02. Área Bruta de Construção		1 709,20
03. Área de Estacionamento		383,29
04. Área Exterior Pavimentada - Cimp. 0.5		987,05
05. Área Aljardizada - Cimp. 0		748,74
06. Área UJH		922,10
07. Área Habitável		699,54

projeto	Edifício do Hospital Militar em
local	Obra de Edificação Militar
localização	Rua do Extremo - Lote 10
características	São Osório, Portugal
referência	UNBIO - Incidência de
data	1920-1923
autor	EX
nome do desenho	Comunicação Privada
data	agosto 2020
autor	José Patrício Fialho
nome do desenho	OH
data	2018
autor	AR
nome do desenho	Desenho Geral
data	11/05
autor	Plano Pios
nome do desenho	RO1
data	
autor	

1.01.005

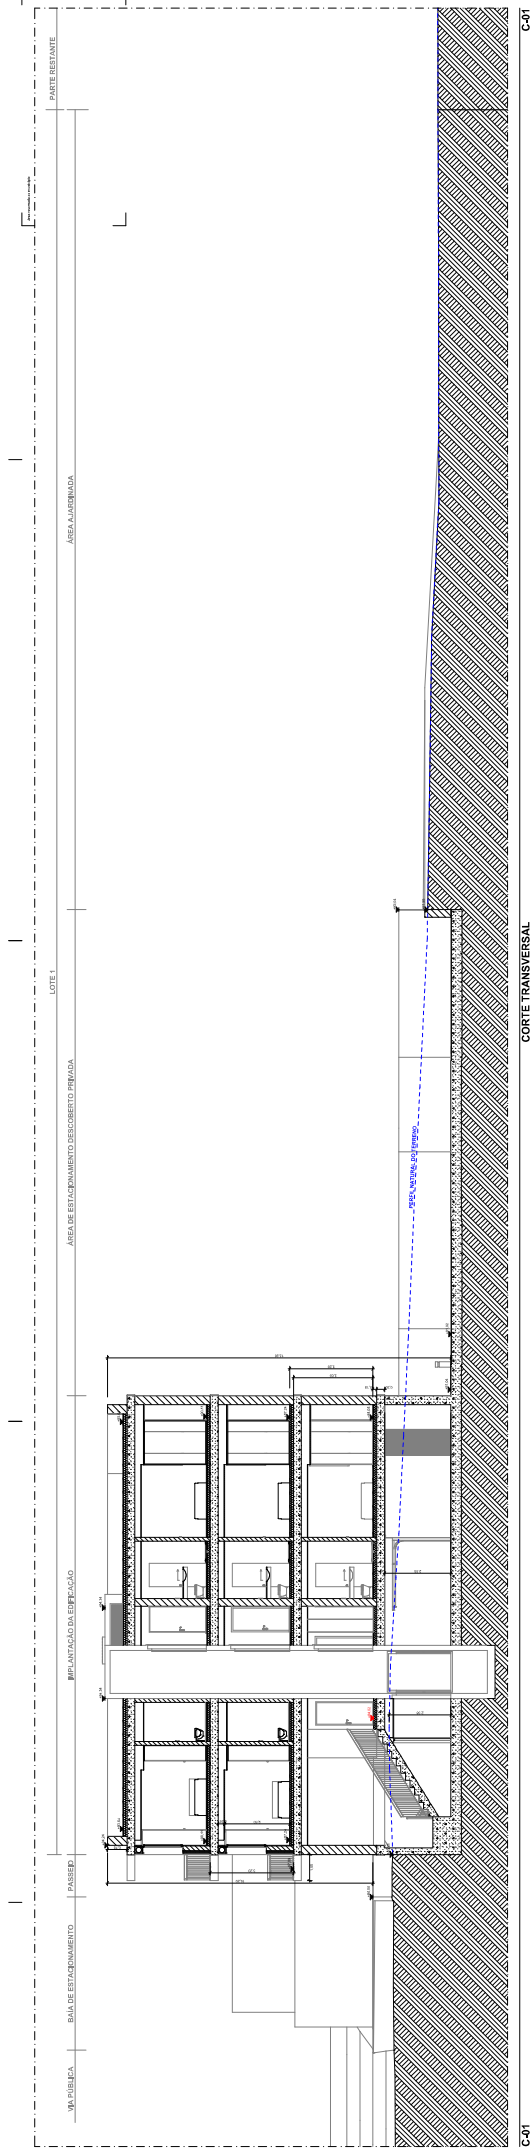

CORTE TRANSVERSAL

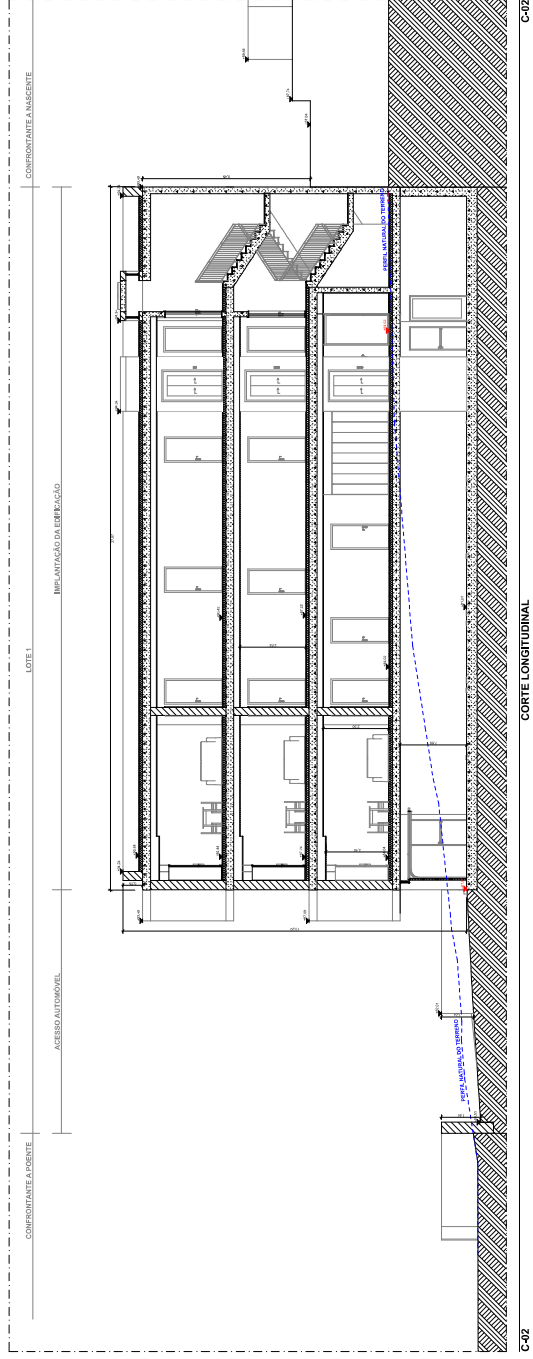


CORTE LONGITUDINAL

[illegible]

ESTE DESENHO É PROPRIEDADE INTELECTUAL DA COTA FRONTAL - EMPREENDIMENTOS IMOBILIÁRIOS, LDA. A SUA REPRODUÇÃO TOTAL OU PARCIAL NÃO É PERMITIDA SEM AUTORIZAÇÃO EXPRESSA DA MESMA. RESERVADOS TODOS OS DIREITOS DE AUTOR. NÃO MEDIR O DESENHO.
THIS DRAWING IS INTELLECTUAL PROPERTY OF COTA FRONTAL - EMPREENDIMENTOS IMOBILIÁRIOS, LDA. ITS PARTIAL OR FULL USE OR DISCLOSURE, IT'S NOT ALLOWED WITHOUT PRIOR CONSENT FROM THE COMPANY. ALL COPYRIGHTS RESERVED. DO NOT MEASURE THE DRAWING.

área reservada ao município

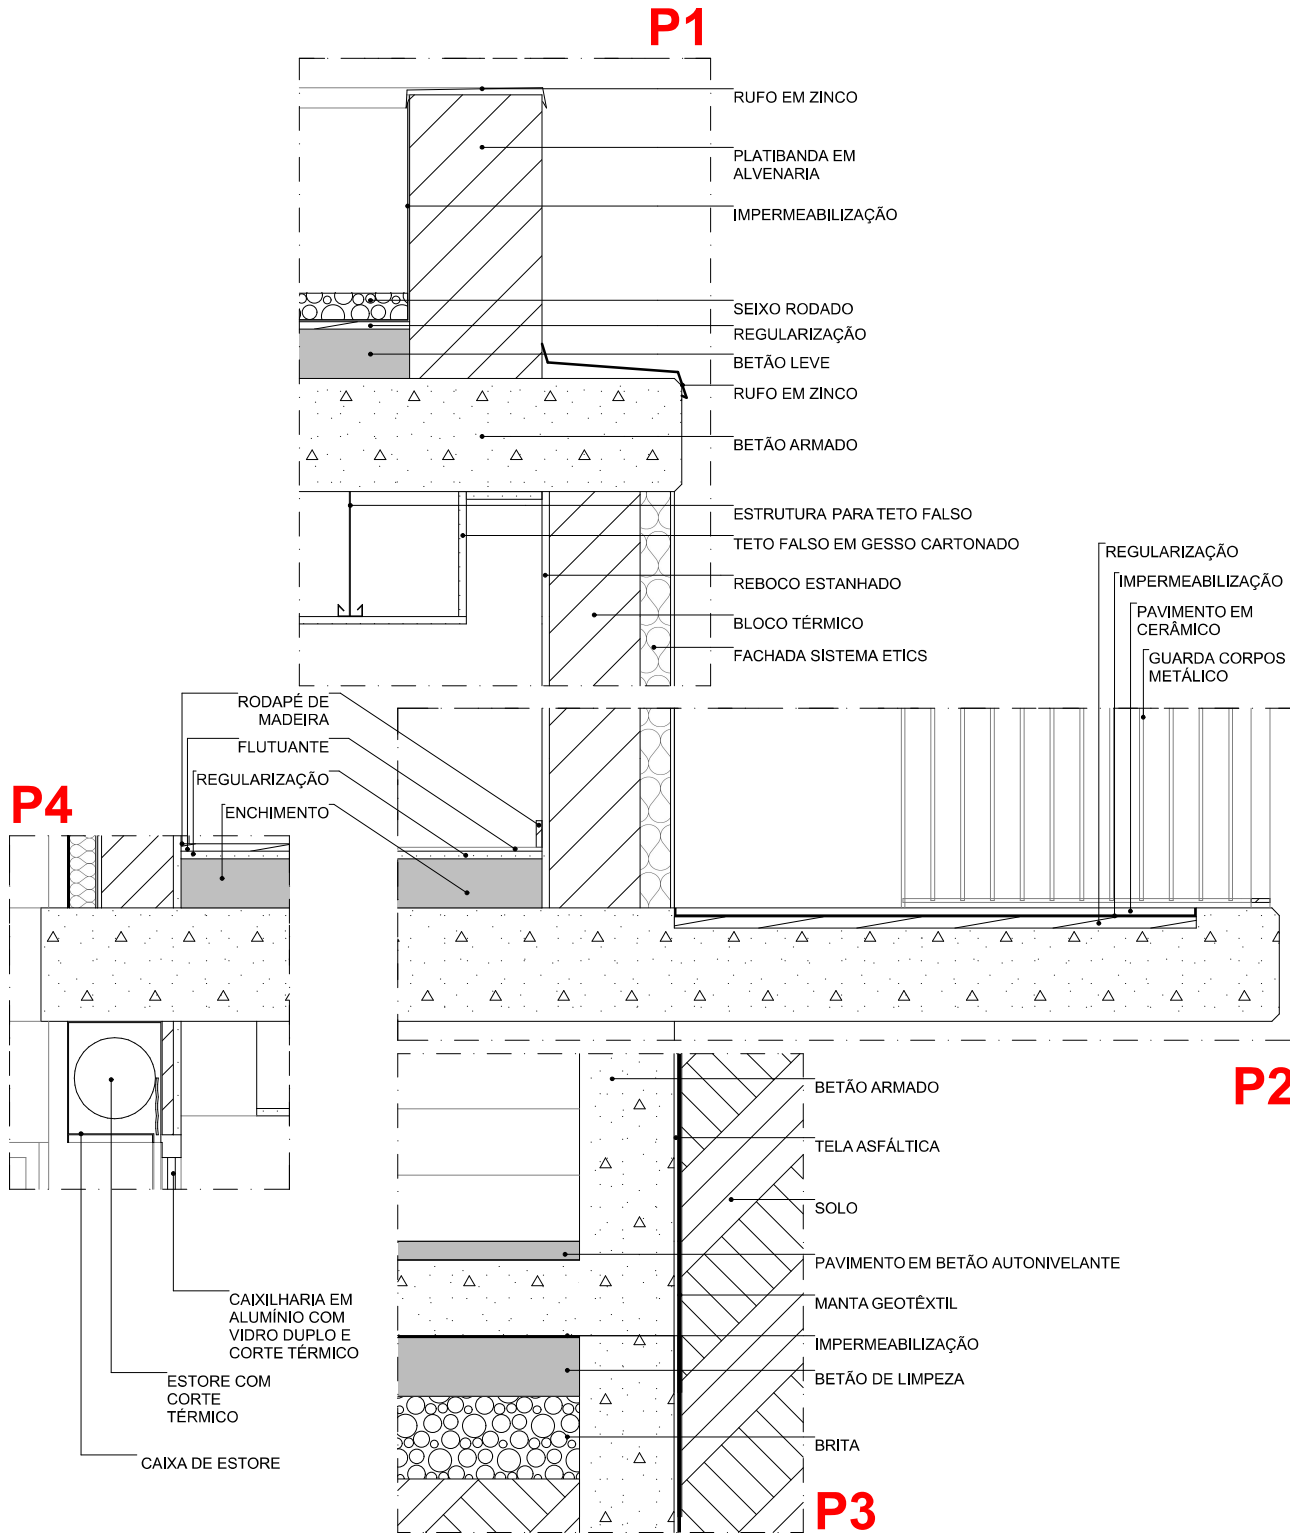

projeto	Edifício de Habitação Multifamiliar
local	Rua da Extrema - Lote1
requerente	UMBAU - Imobiliária e Construção Lda.
referência	Obra de Edificação
local	São Cosme, Portugal
requerente	UMBAU - Imobiliária e Construção Lda.

fase	Comunicação Prévia
data	agosto 2026
autor	João Pelicano Paulos
norte do desenho	OA 28504
escala	1:20

desenho	Pormenorização
revisão	Pormenores Construtivos
folha n.º	R01
3.001	

DADOS DA OPERAÇÃO URBANÍSTICA		
DESIGNAÇÃO	ÁREA (m2)	
00. Área Total - Lote 1	1 800,00	
01. Área de Implantação / Impermeabilização - Cimp. 1	431,60	
02. Área Bruta de Construção	1 709,20	
03. Área de Estacionamento	383,29	
04. Área Exterior Pavimentada - Cimp. 0.5	587,05	
05. Área Ajardinada - Cimp. 0	749,74	
06. Área Útil	922,10	
07. Área Habitável	699,54	

ÁREAS ÚTEIS		
TIPOLOGIA	DIVISÃO	ÁREA (m2)
A	Hall	6,01
	I.S.	3,67
	Quarto	11,00
	Sala / Cozinha	19,80
		40,48 m²
B	I.S.	3,75
	Sala / Cozinha	21,60
		25,35 m²
C	Hall	10,01
	I.S.	3,75
	Quarto	10,72
	Sala / Cozinha	20,10
D	I.S.	4,58
	Sala / Cozinha	29,13
		33,71 m²
E	Hall	6,51
	I.S.	3,75
	Quarto	11,48
	Sala / Cozinha	18,60
F	Hall	4,04
	I.S.	4,21
	Quarto	12,41
	Sala / Cozinha	19,87
G	Hall	3,95
	I.S.	3,64
	Quarto	13,58
	Sala / Cozinha	20,60

ÁREAS ÚTEIS		
TIPOLOGIA	DIVISÃO	ÁREA (m2)
H	I.S.	4,16
	Sala / Cozinha	23,02
	Quarto	27,18 m²
	Hall	4,55
	I.S.	3,75
I	I.S.	3,75
	Quarto	10,73
	Sala / Cozinha	18,25
		37,28 m²
J	Hall	4,65
	I.S.	4,13
	Quarto	10,59
	Sala / Cozinha	18,97
K	Hall	6,15
	I.S.	3,90
	Quarto	11,03
	Sala / Cozinha	17,88
L	Hall	9,86
	I.S.	3,75
	Quarto	10,72
	Sala / Cozinha	20,10
M	I.S.	4,58
	Sala / Cozinha	29,13
		33,71 m²
N	Hall	6,51
	I.S.	3,75
	Quarto	11,48
	Sala / Cozinha	18,60

ÁREAS ÚTEIS		
TIPOLOGIA	DIVISÃO	ÁREA (m2)
O	Hall	4,04
	I.S.	4,21
	Quarto	12,41
	Sala / Cozinha	18,42
		39,08 m²
P	Hall	6,51
	I.S.	3,75
	Quarto	3,95
	Sala / Cozinha	3,64
Q	Hall	4,04
	I.S.	4,21
	Quarto	12,41
	Sala / Cozinha	18,41
R	Hall	3,95
	I.S.	3,64
	Quarto	13,58
	Sala / Cozinha	20,60
S	Hall	6,15
	I.S.	3,90
	Quarto	11,03
	Sala / Cozinha	17,88
T	Hall	9,86
	I.S.	3,75
	Quarto	10,72
	Sala / Cozinha	20,10

ÁREAS ÚTEIS		
TIPOLOGIA	DIVISÃO	ÁREA (m2)
U	I.S.	4,58
	Sala / Cozinha	29,13
		33,71 m²
V	Hall	6,51
	I.S.	3,75
	Quarto	11,48
W	Hall	4,04
	I.S.	4,21
	Quarto	12,41
	Sala / Cozinha	18,41
X	Hall	3,95
	I.S.	3,64
	Quarto	13,58
	Sala / Cozinha	20,60

ÁREAS BRUTAS		
FRAÇÃO	TIPOLOGIA	ÁREA (m2)
A	T1	49,63
B	T0	33,29
C	T1	59,25
D	T0	45,64
E	T1	53,65
F	T1	52,32
G	T1	54,57
H	T0	34,54
I	T1	50,73
J	T1	48,97
K	T1	52,14
L	T1	59,46
M	T0	45,64
N	T1	53,65
O	T1	51,32
P	T1	54,53
Q	T1	50,73
R	T1	48,97
S	T1	52,14
T	T1	59,10
U	T0	45,64
V	T1	53,65
W	T1	51,32
X	T1	54,53

projeto
project

Edifício de Habitação Multifamiliar

Obra de Edificação

local
location

Rua da Extrema - Lote1

responsável
responsable

Soc Cosme Portugal

referência
reference

UMBAU - Imobiliária e Consultoria Lda

fase
phase

Comunicação Prévia

data
date

agosto 2026

autor
author

Julia Pellen e Sofia

aviso de desenho
drawing note

DA 08/2024

escala
scale

desenho
drawing

Mapas e Quadros

revisão
revision

Quadros Sínticos

R01

4.001

ESTE DESENHO É PROPRIEDADE INTELECTUAL DA COTA FRONTAL - EMPREENDIMENTOS IMOBILIÁRIOS, LDA. A SUA REPRODUÇÃO TOTAL OU PARCIAL NÃO É PERMITIDA SEM AUTORIZAÇÃO EXPRESSA DA MESMA. RESERVADOS TODOS OS DIREITOS DE AUTOR. NÃO MEDIR O DESENHO.
THIS DRAWING IS INTELLECTUAL PROPERTY OF COTA FRONTAL - EMPREENDIMENTOS IMOBILIÁRIOS, LDA. ITS PARTIAL OR FULL USE OR DISCLOSURE, IT'S NOT ALLOWED WITHOUT PRIOR CONSENT FROM THE COMPANY. ALL COPYRIGHTS RESERVED. DO NOT MEASURE THE DRAWING.

Área reservada ao município

FRAÇÃO	A	B	C	D	E	F	G	H	I	J	K	L
PISO FRAÇÃO	R/CHÃO	R/CHÃO	R/CHÃO	R/CHÃO	R/CHÃO	R/CHÃO	R/CHÃO	R/CHÃO	1º	1º	1º	1º
PISO ESTACIONAMENTO	CAVE	CAVE	CAVE	CAVE	CAVE	CAVE	CAVE	CAVE	CAVE	CAVE	CAVE	CAVE
DESTINO	HAB.	HAB.	HAB.	HAB.	HAB.	HAB.	HAB.	HAB.	HAB.	HAB.	HAB.	HAB.
TIPOLOGIA	T1	T0	T1	T1	T1	T1	T1	T0	T1	T1	T1	T1
ÁREA FRAÇÃO	50,91	33,29	59,25	45,64	53,65	52,32	55,57	34,54	50,73	48,00	52,14	59,46
ÁREA ESTACIONAMENTO	14,92	14,92	14,92	14,92	14,92	14,92	14,92	14,92	14,92	14,92	14,92	14,92
ÁREA TOTAL	65,83	48,21	74,17	60,56	68,57	67,24	70,49	49,46	65,65	62,92	67,06	74,38
VARANDAS			4,14	3,70	3,24	3,24	3,00		4,80	3,00	4,80	4,50
PERMILAGEM	41,75	30,57	47,04	38,41	43,49	42,64	44,70	31,37	41,63	39,90	42,53	47,17

FRAÇÃO	M	N	O	P	Q	R	S	T	U	V	W	X
PISO FRAÇÃO	1º	1º	1º	1º	2º	2º	2º	2º	2º	2º	2º	2º
PISO ESTACIONAMENTO	CAVE	CAVE	CAVE	CAVE	CAVE	CAVE	CAVE	CAVE	CAVE	CAVE	CAVE	CAVE
DESTINO	HAB.	HAB.	HAB.	HAB.	HAB.	HAB.	HAB.	HAB.	HAB.	HAB.	HAB.	HAB.
TIPOLOGIA	T0	T1	T1	T1	T1	T1	T1	T1	T0	T1	T1	T1
ÁREA FRAÇÃO	46,64	53,65	51,32	55,53	50,73	47,97	52,14	59,10	45,64	53,65	51,32	55,53
ÁREA ESTACIONAMENTO	14,92	14,92	14,92	14,92	14,92	14,92	14,92	14,92	14,92	14,92	14,92	14,92
ÁREA TOTAL	61,56	68,57	66,24	70,45	65,65	62,89	67,06	74,02	60,56	68,57	66,24	70,45
VARANDAS	4,05	3,24	3,24	3,00	4,80	3,00	4,80	4,14	3,70	3,24	3,24	3,00
PERMILAGEM	39,04	43,49	42,01	44,68	41,63	39,88	42,53	46,94	38,41	43,49	42,01	44,68

projeto	Edifício de Habitação Multifamiliar
project	Obra de Edificação
local	Rua da Extrema - Lote1
location	São Cosme, Portugal
requerente	UMBAU - Imobiliária e
applicant	Construção Lda.

referência	EXT
reference	
fase	Comunicação Prévia
phase	
data	agosto 2026
date	
autor	João Pelicano Paulos
author	OA 28504
norte do desenho	
drawing north	
escala	
scale	

desenho	Mapas e Quadros
drawing	
revisão	Permilagem da Propriedade
review	Horizontal
folha n.º	R01
sheet no.	
	4.002