

Área reservada ao município


LEGENDA
— Limite do terreno descrito na
1ª Conservatória do Registo
Predial de Vila Nova de Gaia
sob o nº 43009, art. matricial
nº 9814 e uma área de
548,58 m²

548.58m²


RUA

AP

TQ

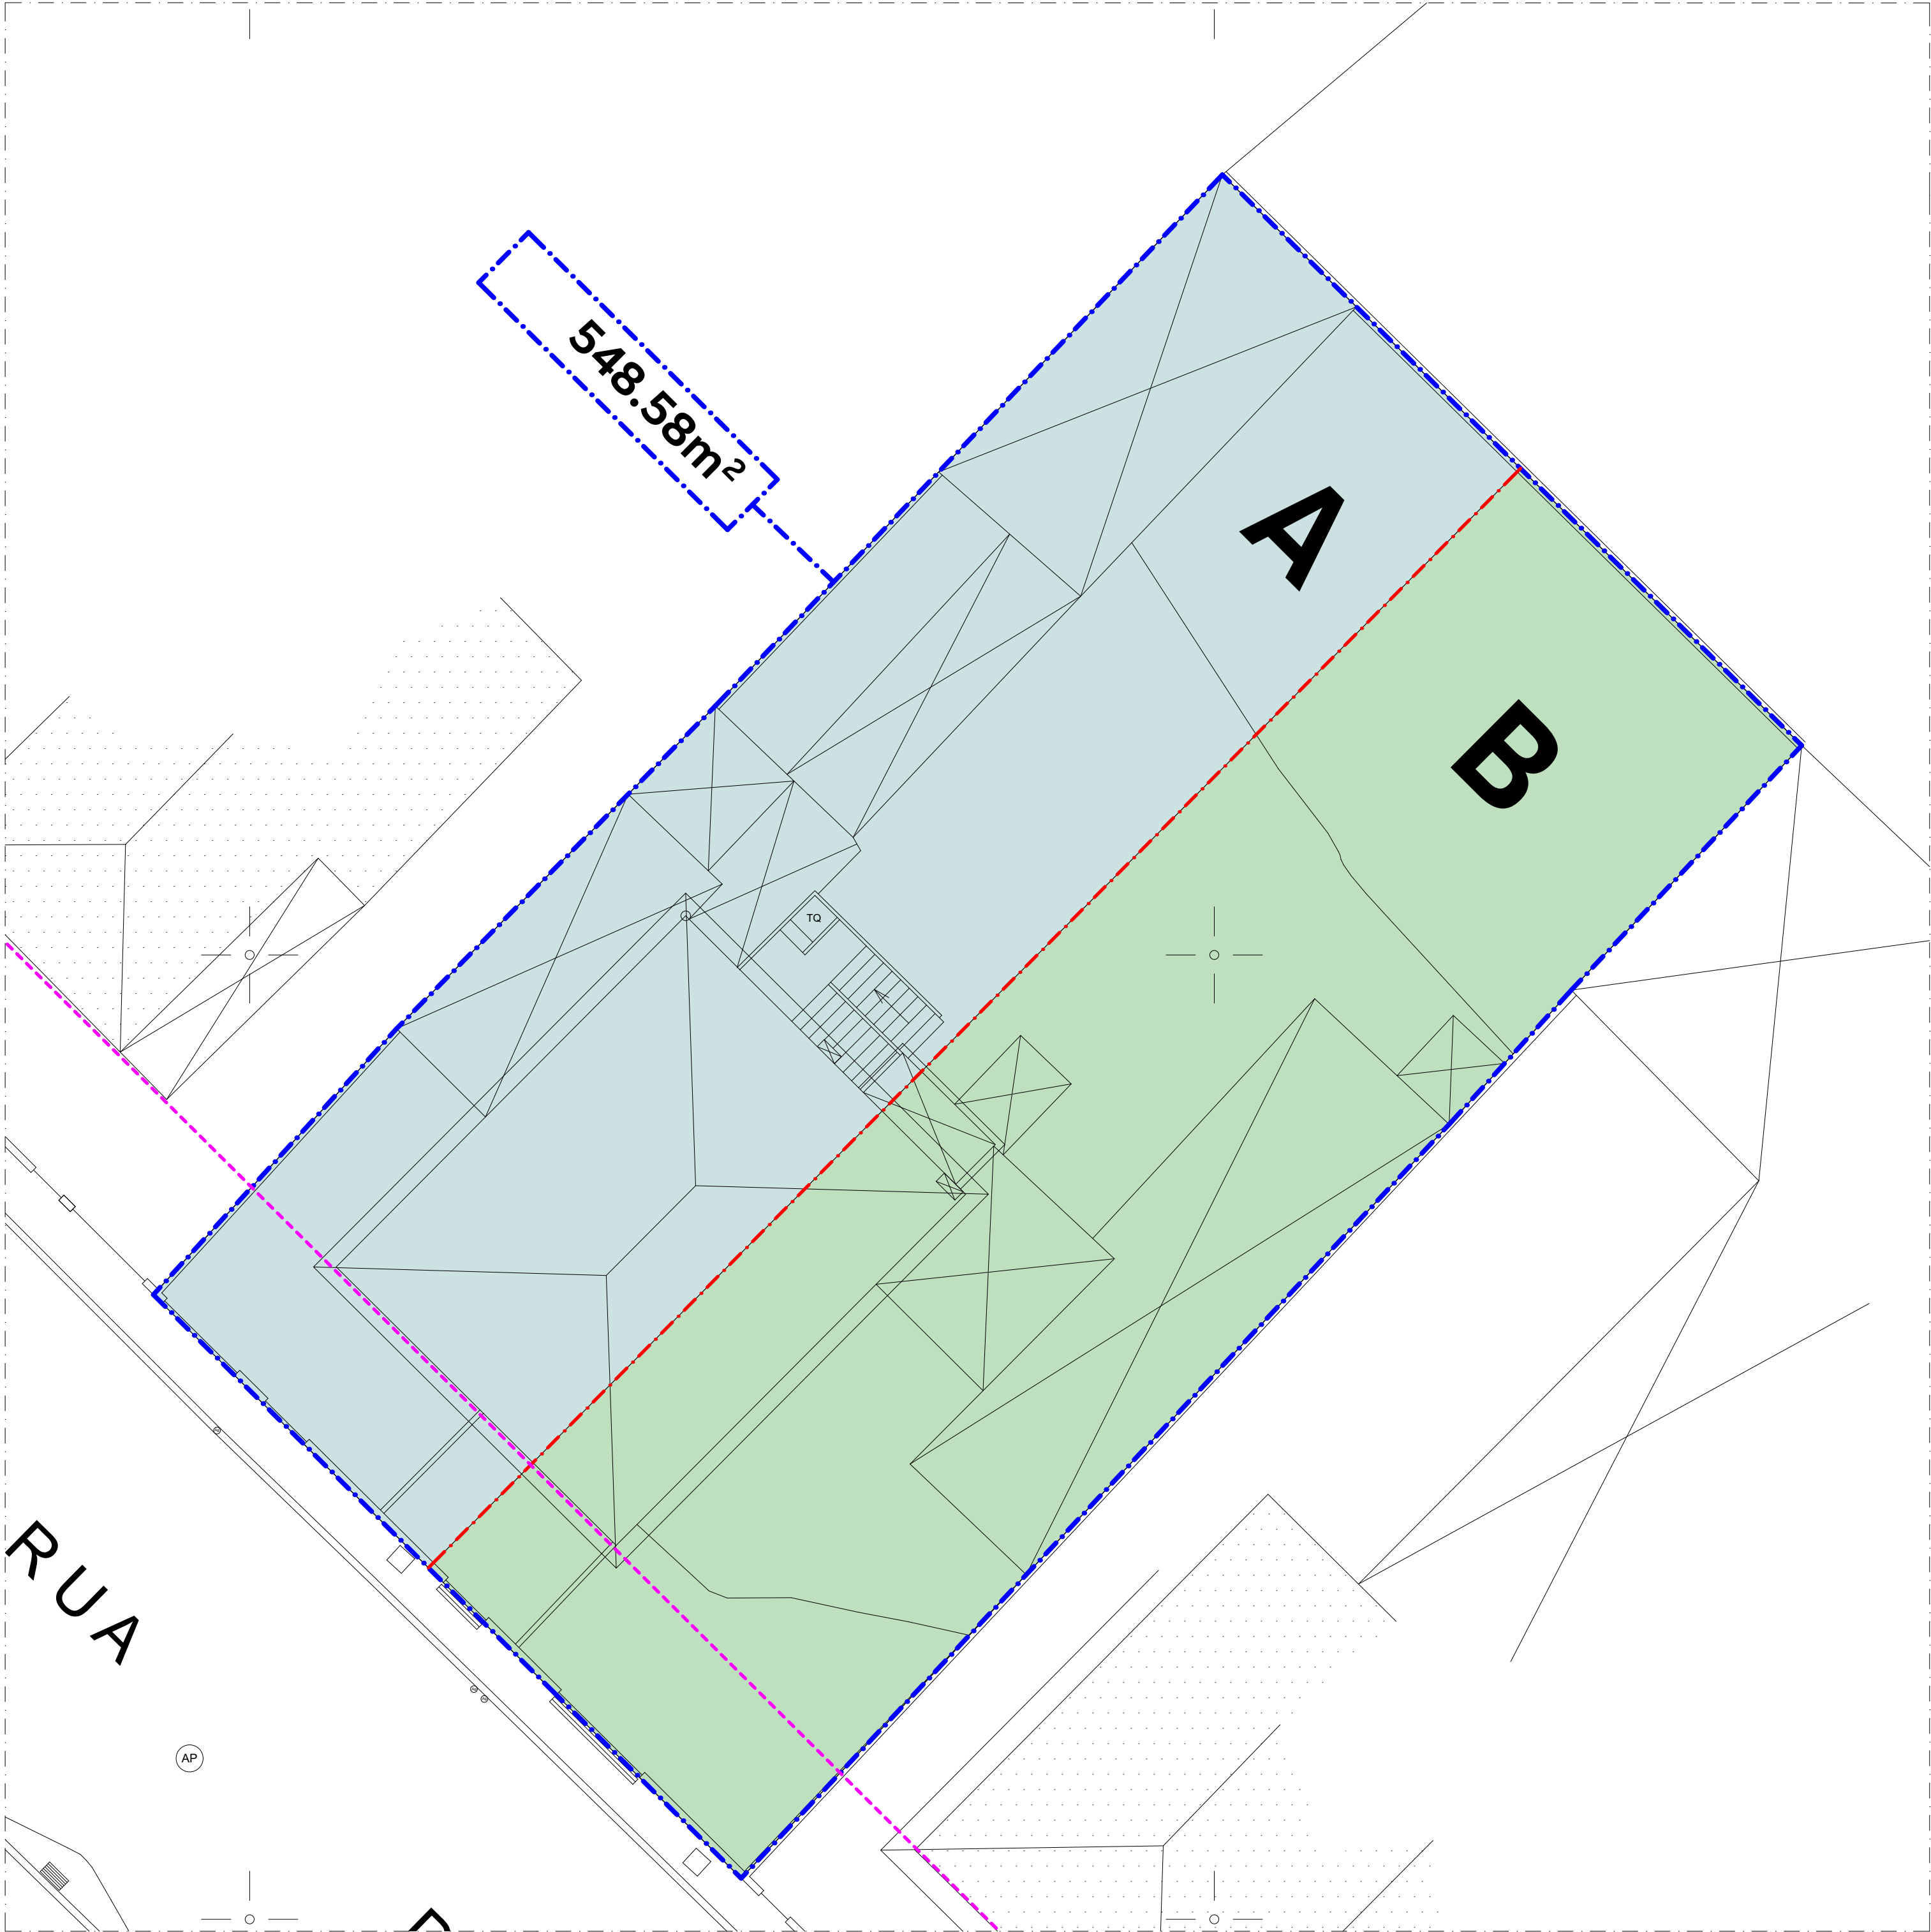


LEGENDA

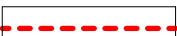-  Limite do terreno descrito na 1ª Conservatória do Registo Predial de Vila Nova de Gaia sob o nº 43009, art. matricial nº3614 e uma área de 548.58 m²
-  Linha de divisão para o destaque
-  Cadastro A: 269.81m² - Terreno a destacar do prédio 43009/3614 (548.58 m2)
-  Cadastro B: 278.76m² - Terreno a destacar do prédio 43009/3614 (548.58 m2)



Ortofotomapa com implantação das construções propostas para as parcelas A e B

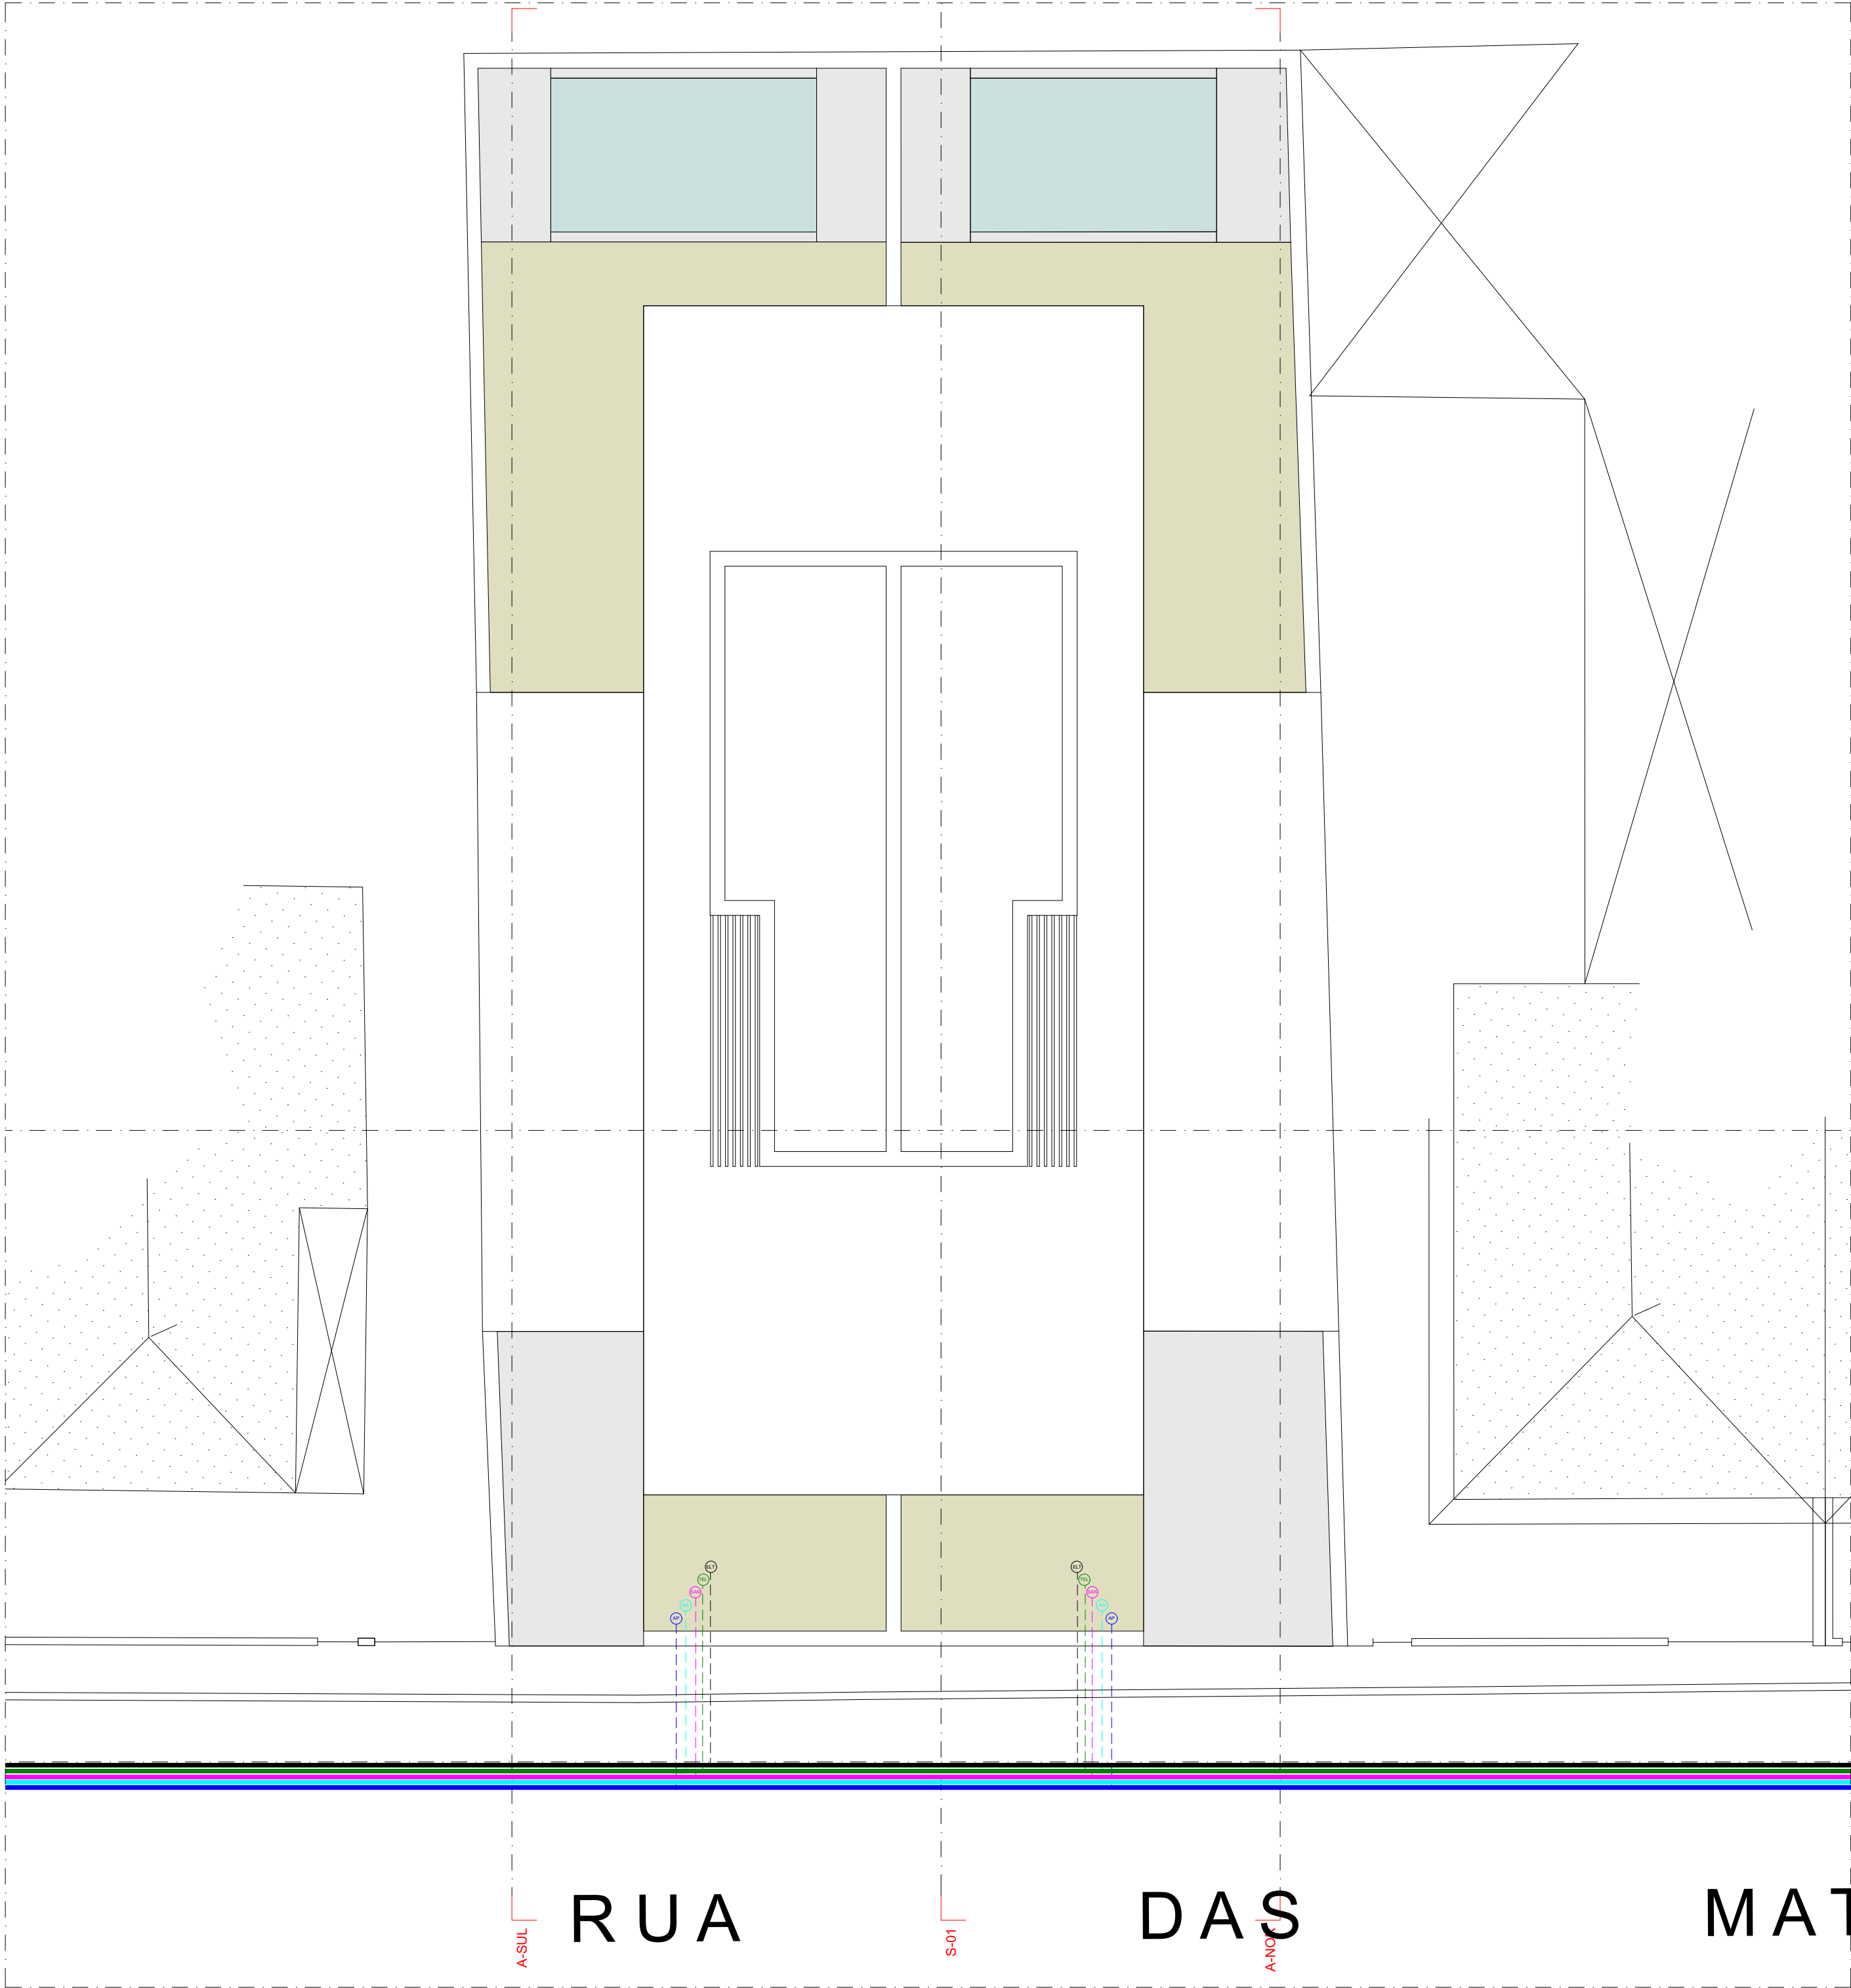


LEGENDA

- Limite do prédio
- Linha de afastamento de 3m
- Alinhamentos definidos de acordo com a planta de alinhamentos
- Ligação à rede de águas pluviais
- Ligação à rede de abastecimento de água
- Ligação à rede de telecomunicações
- Ligação à rede de média tensão
- Ligação à rede de saneamento

Quadro de Áreas Geral	
Descrição	Área m2
01. Área Total do Prédio Existente	548,58
02. Área de Implantação Proposta	300,27
02.1 Área de Implantação Existente	84,12
02.2 Área de Implantação Existente (anexos)	142,29
03. Área Bruta de Construção	538,72
04. Área de Estacionamento	97,55
05. Área de Impermeabilização	24,09
05.1. Área Exterior Coberta (terraços)	14,73
05.2. Área Exterior Coberta (varandas)	25,31
06. Área Verde	115,86
07. Área de Piscina	36,12
08. Área Exterior Pavimentada	84,45
09. Área Útil	413,64
10. Área Habitável	252,98

LEGENDA

- Limite do prédio
- Linha de afastamento de 3m
- Alinhamentos definidos de acordo com a planta de alinhamentos
- Área de implantação (Cimp. = 1)
- Solo permeável Cimp. = 0
- Área de Piscina
- Solo semipermeável Cimp. = 0.5

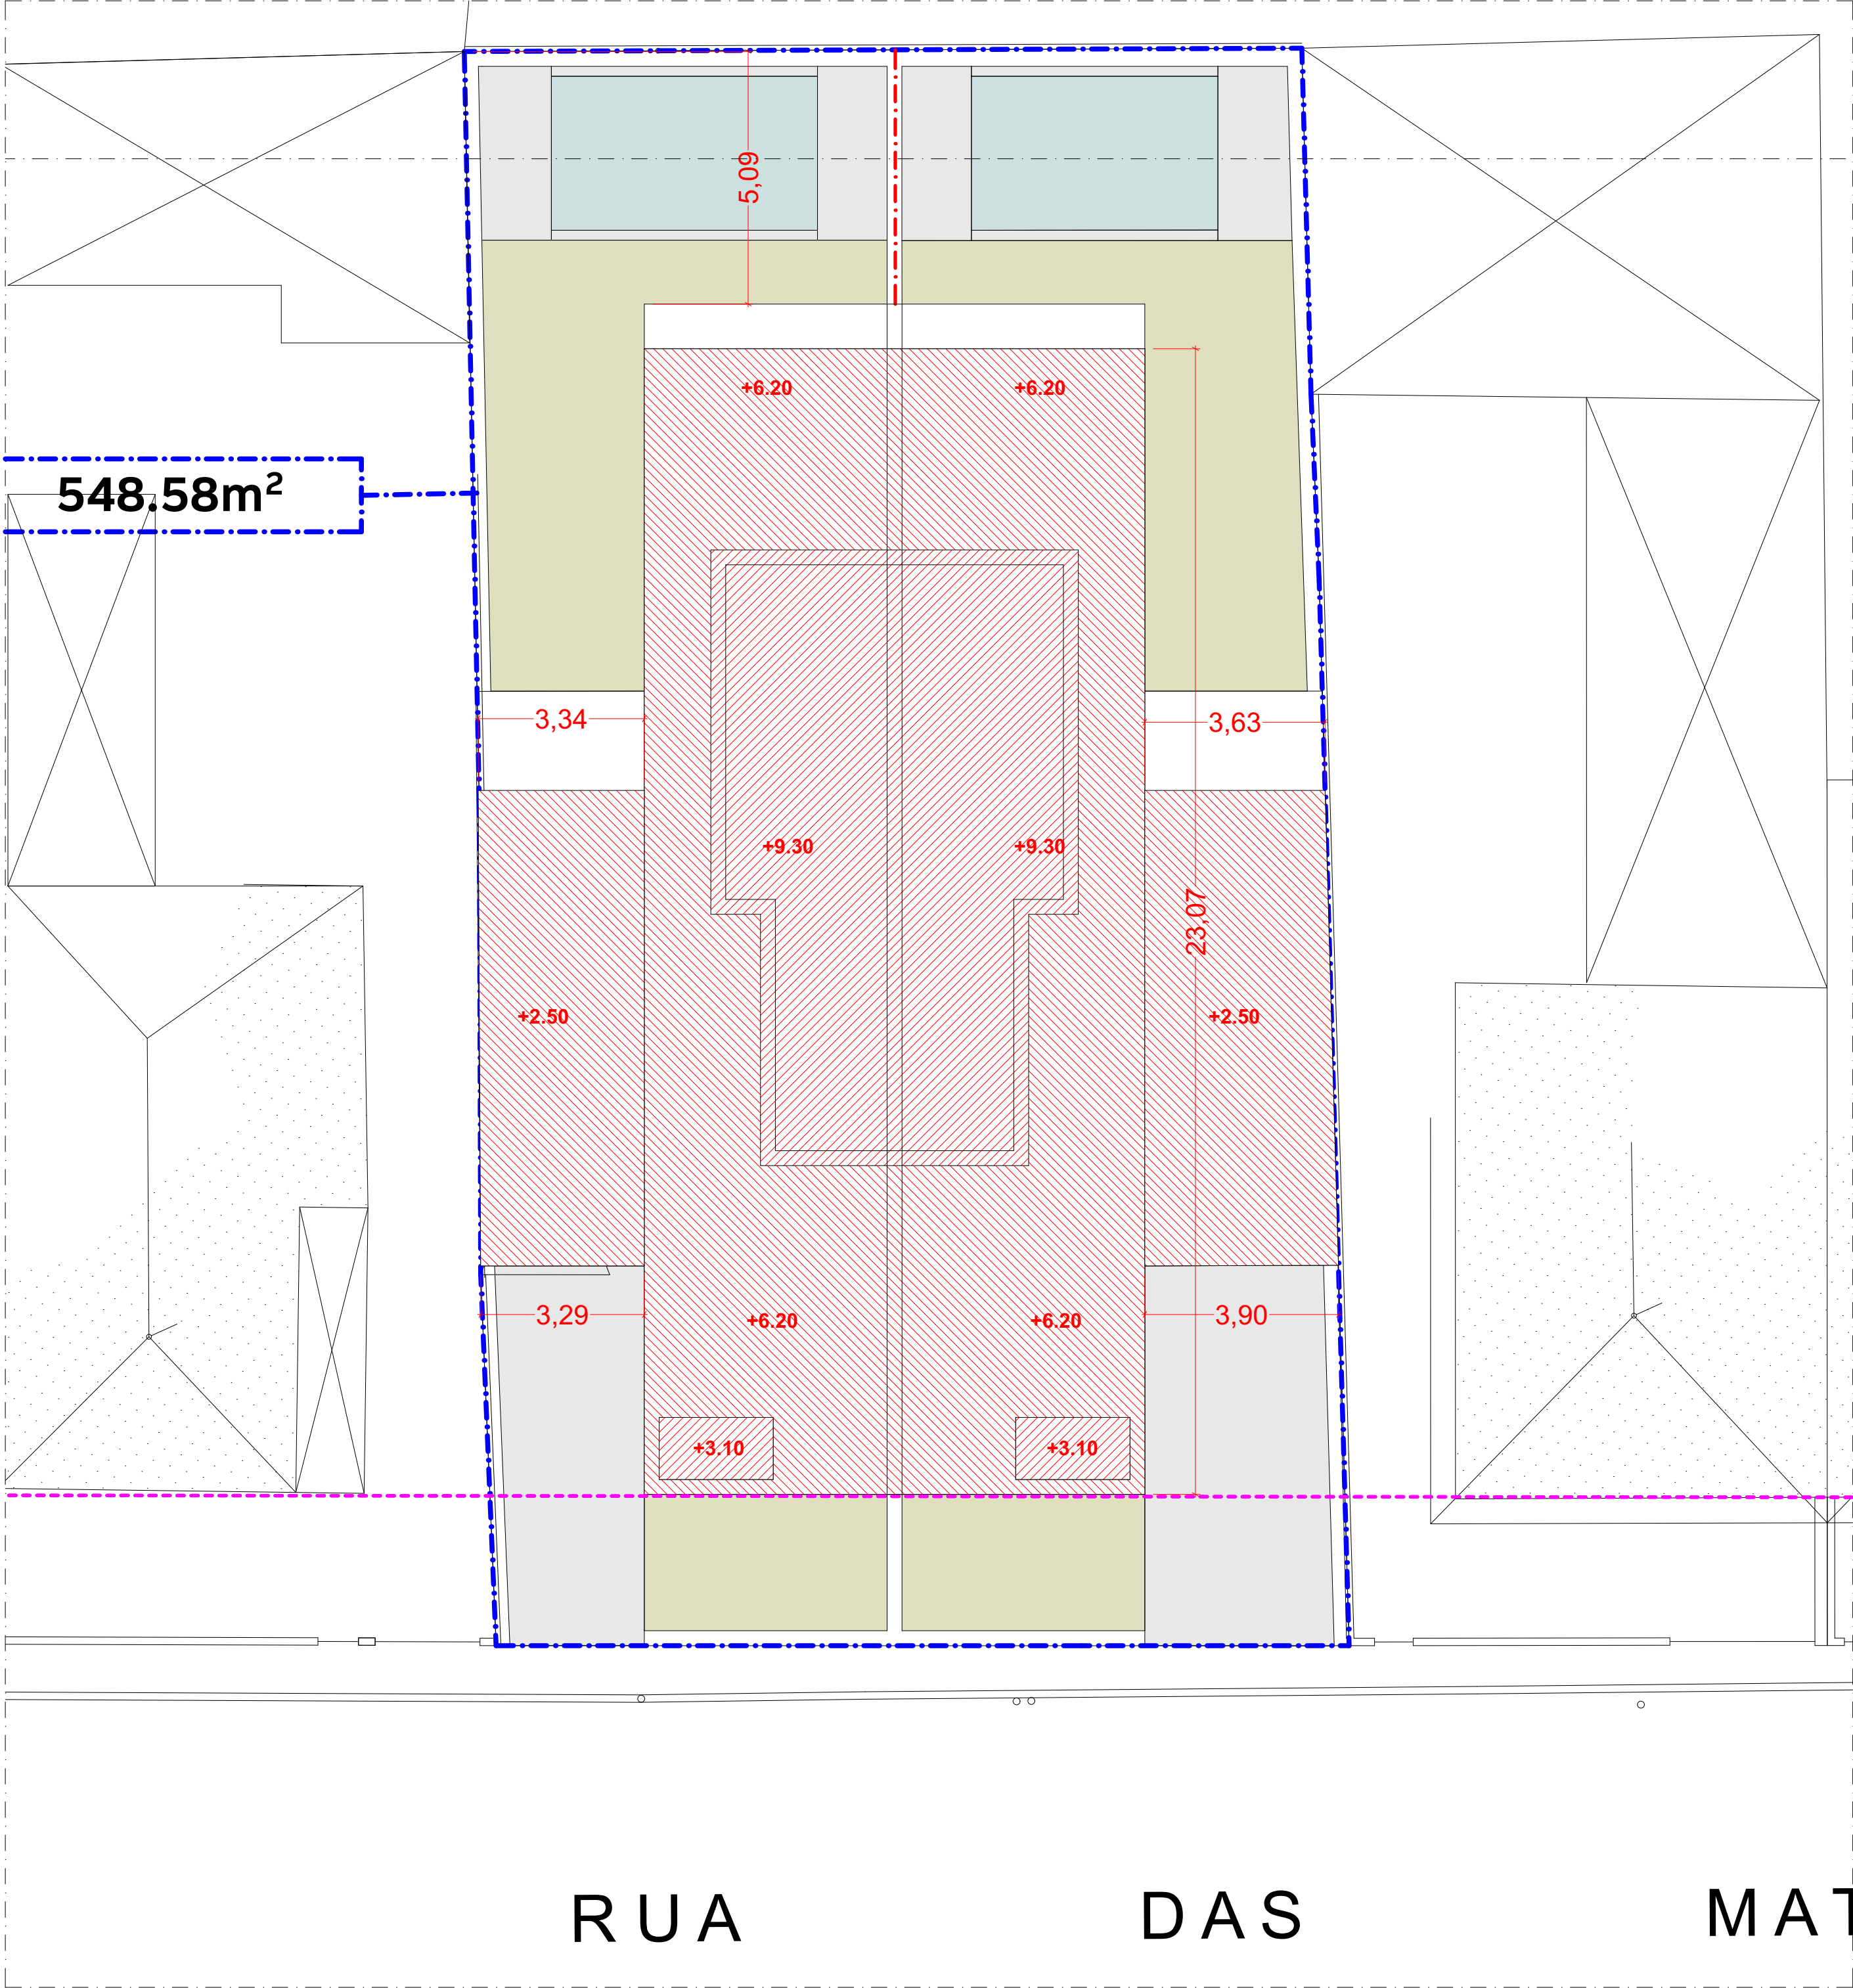


LEGENDA

- Limite do prédio
- Linha de afastamento de 3m
- Alinhamentos definidos de acordo com a planta de alinhamentos
- Área de implantação (Cimp. = 1)
- Solo permeável Cimp. = 0
- Área de Piscina
- Solo semipermeável Cimp. = 0.5

Quadro de Áreas Geral

Descrição	Área m2
01. Área Total do Prédio Existente	548,58
02. Área de Implantação Proposta	300,27
02.1 Área de Implantação Existente	84,12
02.2 Área de Implantação Existente (anexos)	142,29
03. Área Bruta de Construção	538,72
04. Área de Estacionamento	97,55
05. Área de Impermeabilização	24,09
05.1. Área Exterior Coberta (terraços)	14,73
05.2. Área Exterior Coberta (varandas)	25,31
06. Área Verde	115,86
07. Área de Piscina	36,12
08. Área Exterior Pavimentada	84,45
09. Área Útil	413,64
10. Área Habitável	252,98

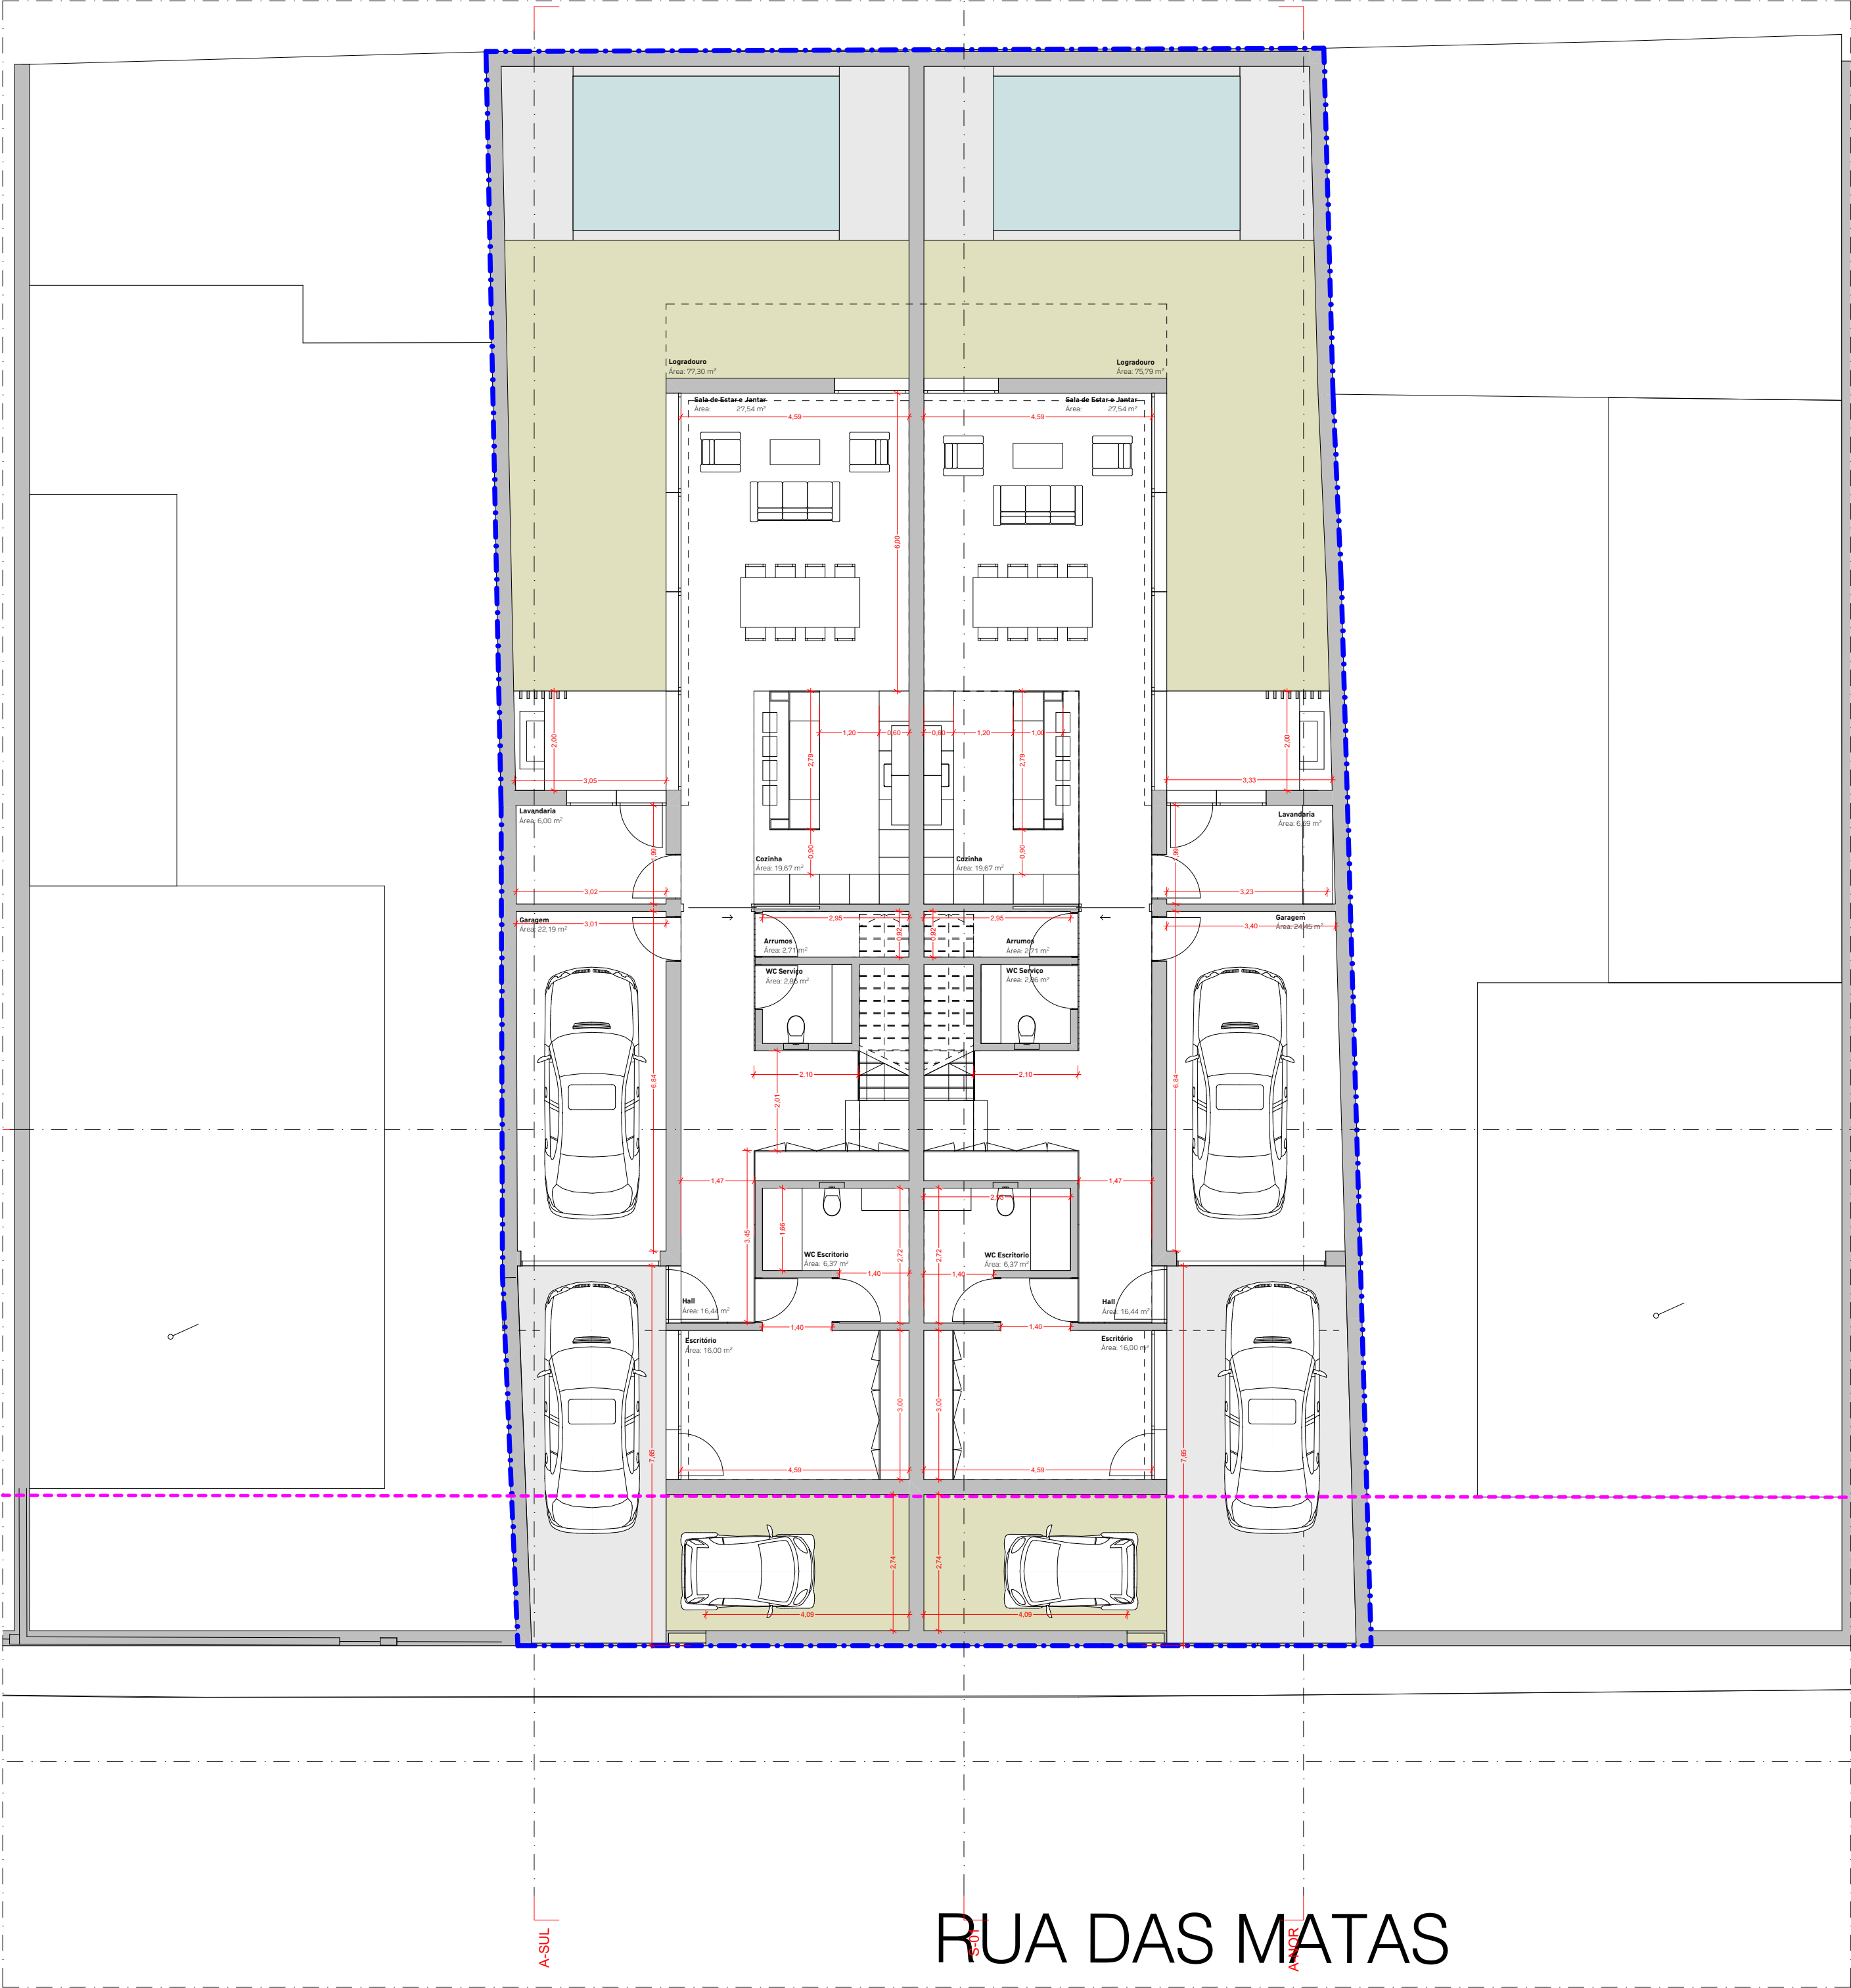

QUADROS SINÓTICOS - Áreas Brutas

Quadro de Áreas Casa 1		
Piso	Designação	Área
Piso 0		
	03. Área Bruta de Construção	119,21
	05.1. Área Exterior Coberta (terraços)	12,73
		131,94 m²
Piso 1		
	03. Área Bruta de Construção	108,75
	05.2. Área Exterior Coberta (varandas)	22,30
		131,06 m²
Piso 2		
	03. Área Bruta de Construção	40,81
		40,81 m²
		303,81 m²

Quadro de Áreas Casa 2		
Piso	Designação	Área
Piso 0		
	03. Área Bruta de Construção	120,38
	05.1. Área Exterior Coberta (terraços)	12,73
		133,11 m²
Piso 1		
	03. Área Bruta de Construção	108,75
	05.2. Área Exterior Coberta (varandas)	22,30
		131,05 m²
Piso 2		
	03. Área Bruta de Construção	40,81
		40,81 m²
		304,97 m²

QUADROS SINÓTICOS - Áreas Úteis

Quadro de Áreas Casa 1		
Piso	Designação	Área
Piso 0		
	Arrumos	2,71
	Cozinha	19,67
	Escritório	16,00
Piso 1		
	Garagem	22,19
	Hall	16,44
	Lavanderia	6,00
Piso 2		
	Logradouro	77,30
	WC Escritório	6,37
	WC Serviço	2,86
		169,54 m²

Quadro de Áreas Casa 2		
Piso	Designação	Área
Piso 0		
	Arrumos	2,71
	Cozinha	19,67
	Escritório	16,00
Piso 1		
	Garagem	24,45
	Hall	16,44
	Lavanderia	6,69
Piso 2		
	Logradouro	75,79
	WC Escritório	6,37
	WC Serviço	2,86
		170,98 m²


Quadro de Áreas Casa 3		
Piso	Designação	Área
Piso 0		
	Circulação	18,49
	Quarto Suite 1	18,68
	Quarto Suite 2	12,94
Piso 1		
	Quarto Suite 3	19,06
	Varanda Frente	3,56
	Varanda Lateral	3,46
Piso 2		
	Varanda Traseiras	4,13
	WC Suite 1	5,34
	WC Suite 2	5,48
	WC Suite 3	5,43
		96,57 m²

Quadro de Áreas Casa 4		
Piso	Designação	Área
Piso 0		
	Sala	22,57
		22,57 m²
		288,68 m²

Quadro de Áreas Casa 5		
Piso	Designação	Área
Piso 0		
	Sala	22,57
		22,57 m²
		290,11 m²

QUADROS SINÓTICOS - Parâmetros Urbanísticos

Descrição	Área m2
01. Área Total do Prédio Existente	548,58
02. Área de Implantação Proposta	300,27
02.1 Área de Implantação Existente	84,12
02.2 Área de Implantação Existente (anexos)	142,29
03. Área Bruta de Construção	538,72
04. Área de Estacionamento	97,55
05. Área de Impermeabilização	24,09
05.1. Área Exterior Coberta (terraços)	14,73
05.2. Área Exterior Coberta (varandas)	25,31
06. Área Verde	115,86
07. Área de Piscina	36,12
08. Área Exterior Pavimentada	84,45
09. Área Útil	413,64
10. Área Habitável	252,98

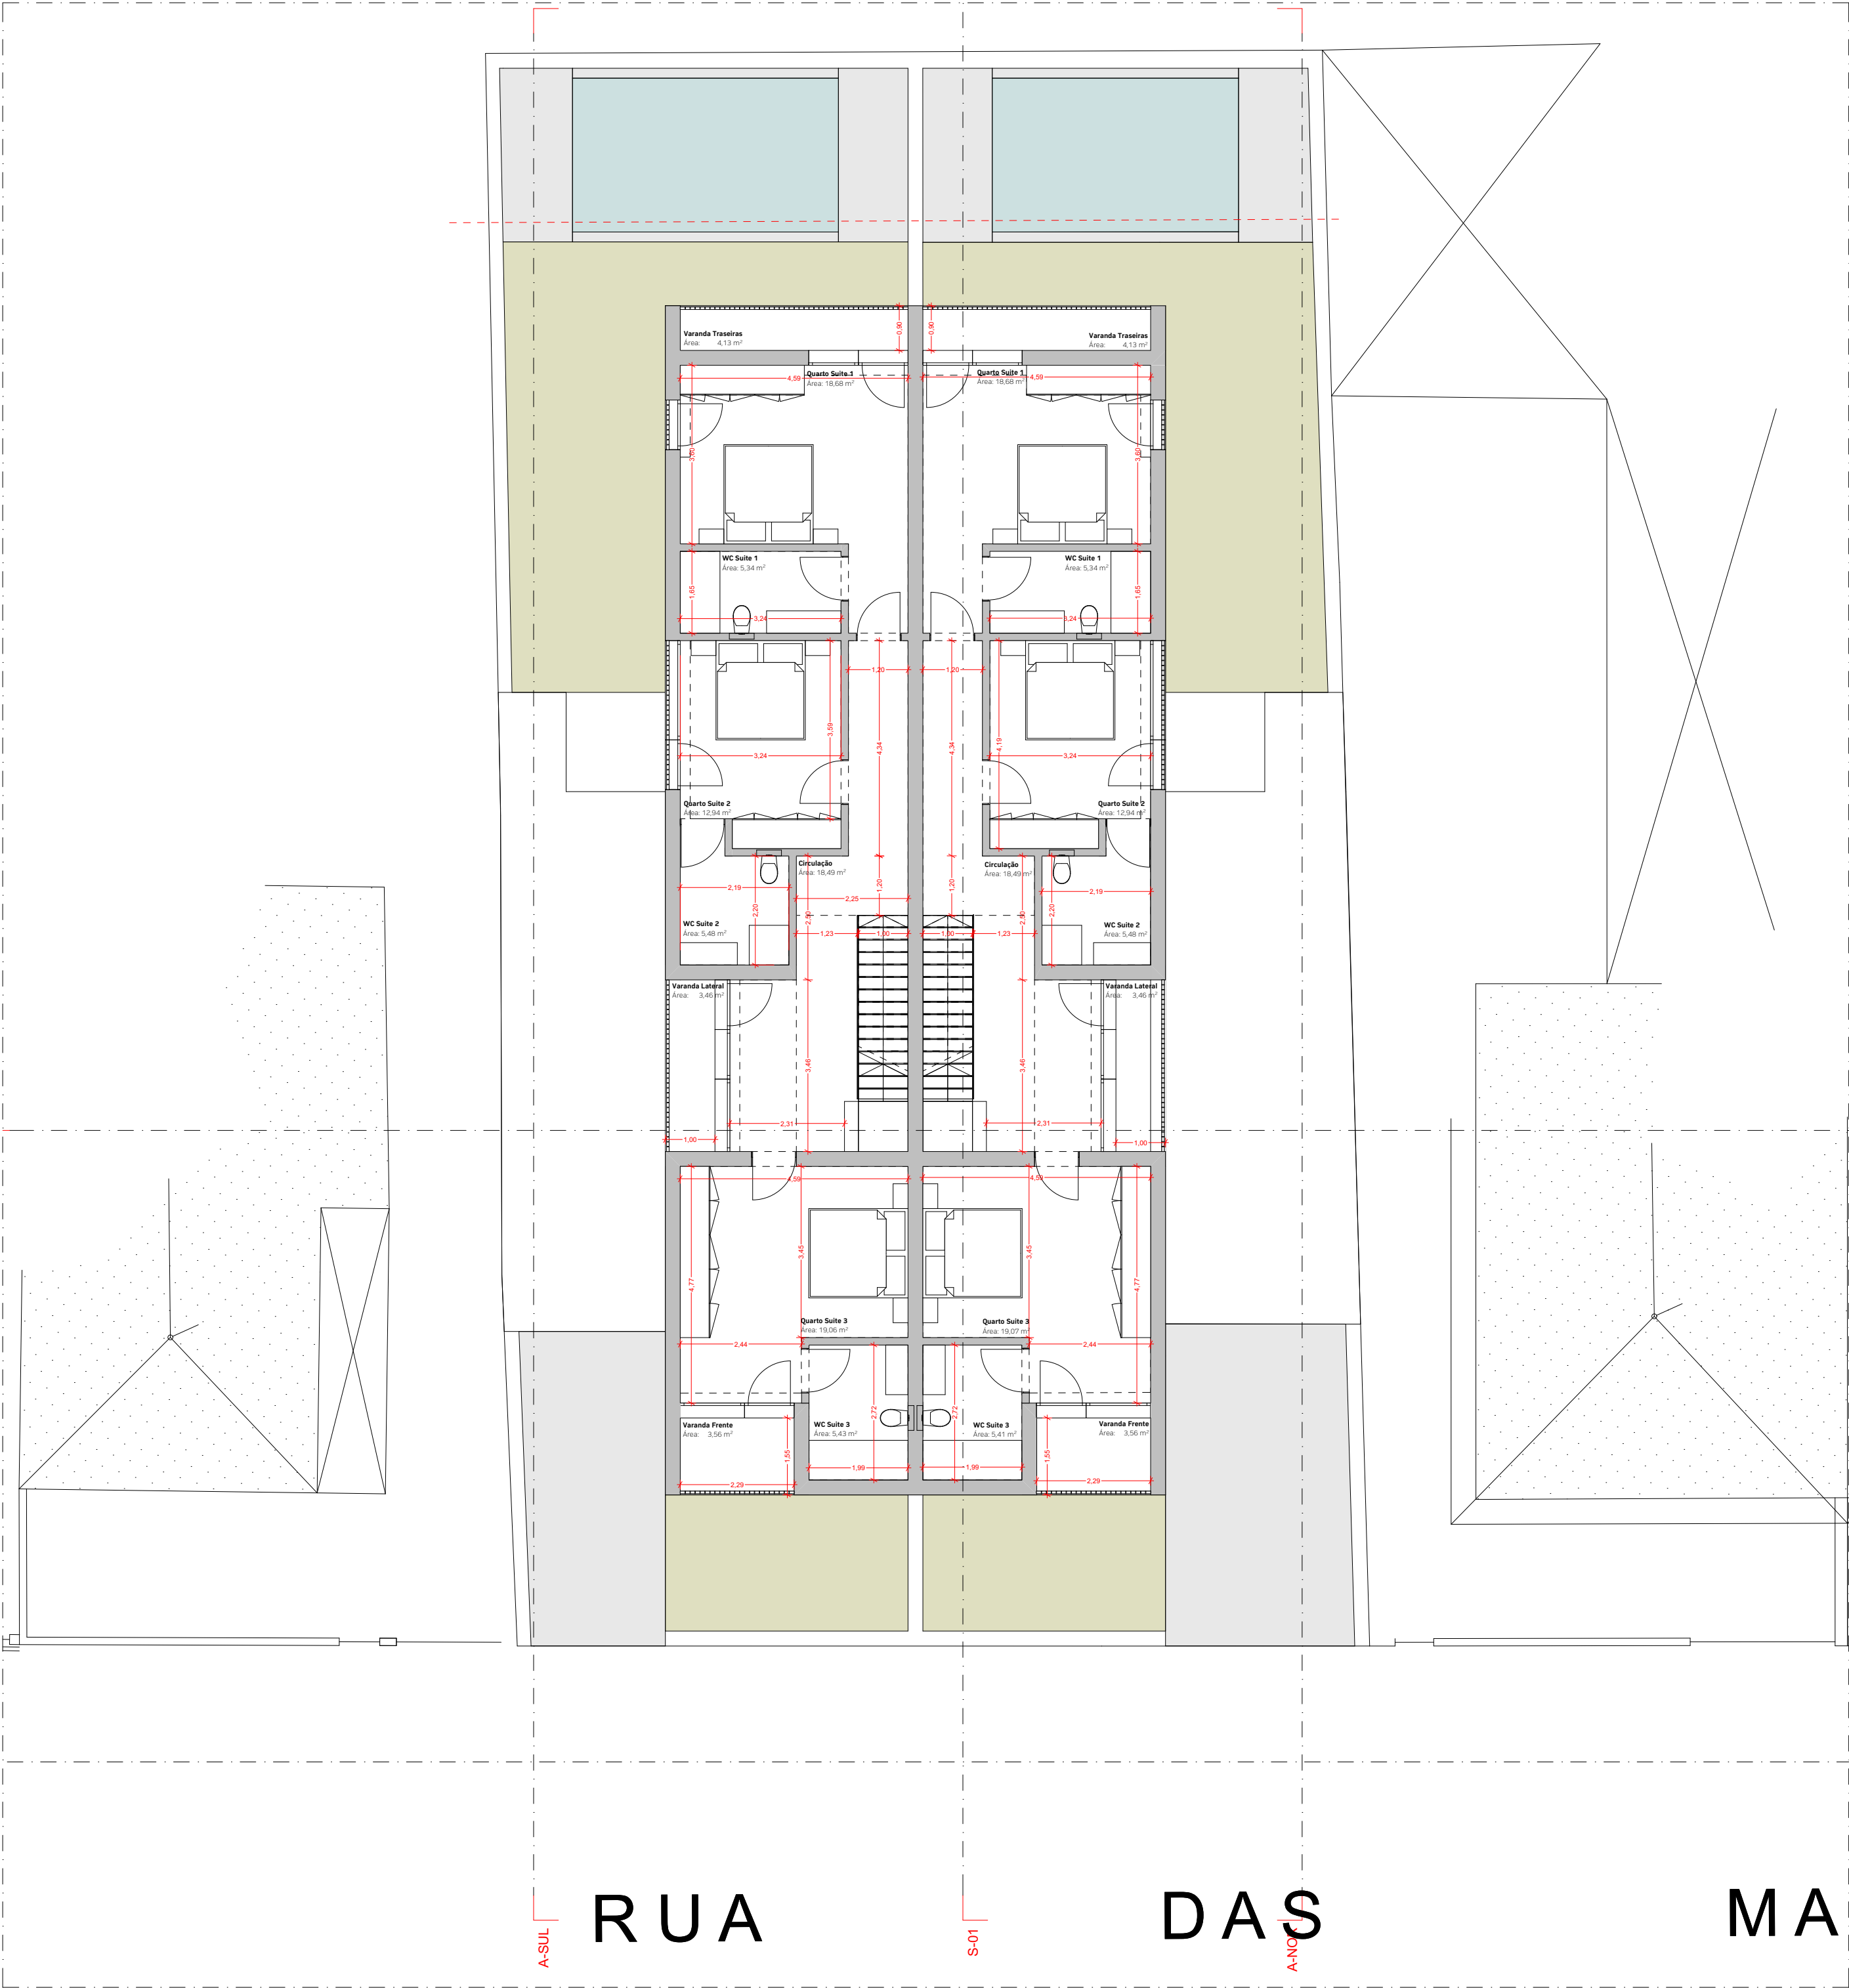

QUADROS SINÓTICOS - Áreas Brutas


Quadro de Áreas Casa 1		
Piso	Designação	Área
Piso 0	03. Área Bruta de Construção	119,21
	05.1. Área Exterior Coberta (terraços)	12,73
		131,94 m²
Piso 1	03. Área Bruta de Construção	108,75
	05.2. Área Exterior Coberta (varandas)	22,30
		131,06 m²
Piso 2	03. Área Bruta de Construção	40,81
		40,81 m²
		303,81 m²
Quadro de Áreas Casa 2		
Piso	Designação	Área
Piso 0	03. Área Bruta de Construção	120,38
	05.1. Área Exterior Coberta (terraços)	12,73
		133,11 m²
Piso 1	03. Área Bruta de Construção	108,75
	05.2. Área Exterior Coberta (varandas)	22,30
		131,05 m²
Piso 2	03. Área Bruta de Construção	40,81
		40,81 m²
		304,97 m²

QUADROS SINÓTICOS - Áreas Úteis

Quadro de Áreas Casa 1		
Piso	Designação	Área
Piso 0	Árums	2,71
	Cozinha	19,67
	Escritório	16,00
	Garagem	22,19
	Hall	16,44
	Lavandaria	6,00
	Logradouro	77,30
	WC Escritório	6,37
Piso 1	WC Serviço	2,86
		169,54 m²
Piso 2	Circulação	18,49
	Quarto Suite 1	18,68
	Quarto Suite 2	12,94
	Quarto Suite 3	19,06
	Varanda Frente	3,56
	Varanda Lateral	3,46
	Varanda Traseiras	4,13
	WC Suite 1	5,34
Piso 1	WC Suite 2	5,48
	WC Suite 3	5,43
Piso 2	Sala	22,57
		22,57 m²
Piso 0		170,98 m²
		290,11 m²

QUADROS SINÓTICOS - Parâmetros Urbanísticos

Descrição	Área m2
01. Área Total do Prédio Existente	548,58
02. Área de Implantação Proposta	300,27
02.1 Área de Implantação Existente	84,12
02.2 Área de Implantação Existente (anexos)	142,29
03. Área Bruta de Construção	538,72
04. Área de Estacionamento	97,55
05. Área de Impermeabilização	24,09
05.1. Área Exterior Coberta (terraços)	14,73
05.2. Área Exterior Coberta (varandas)	25,31
06. Área Verde	115,86
07. Área de Piscina	36,12
08. Área Exterior Pavimentada	84,45
09. Área Útil	413,64
10. Área Habitável	252,98

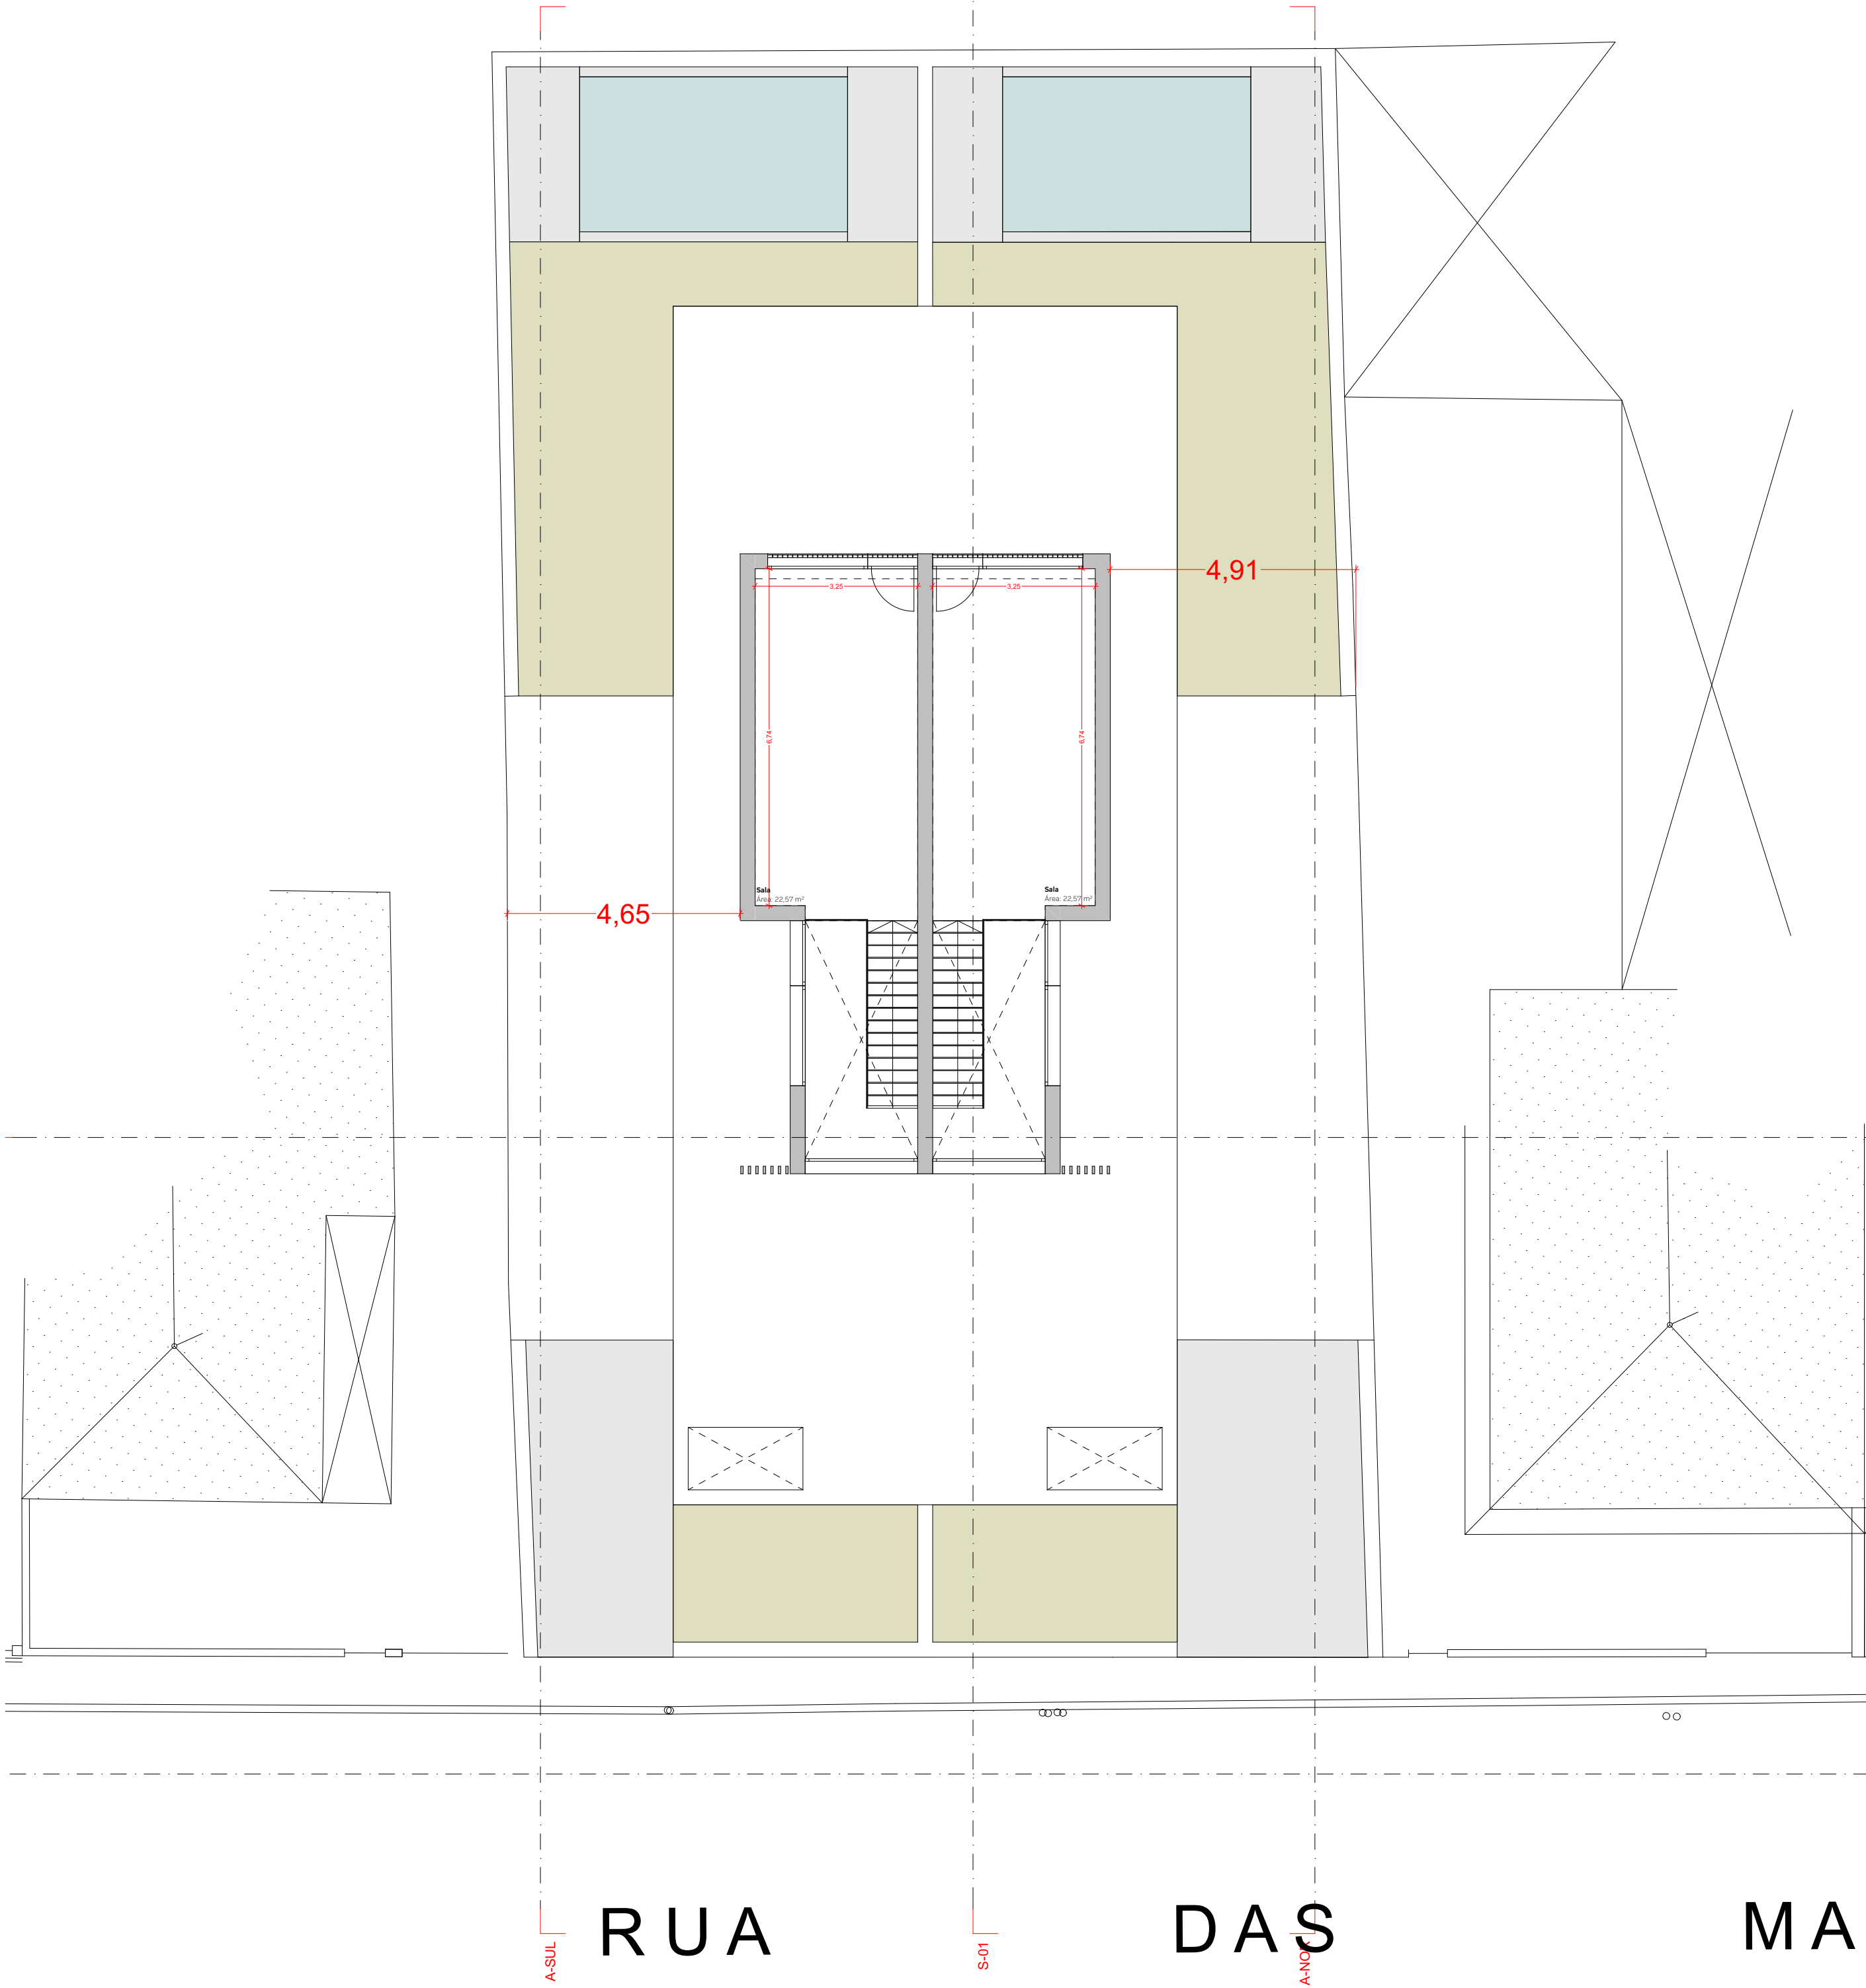

QUADROS SINÓTICOS - Áreas Brutas

Quadro de Áreas Casa 1		
Piso	Designação	Área
Piso 0		
	03. Área Bruta de Construção	119,21
	05.1. Área Exterior Coberta (terraços)	12,73
		131,94 m²
Piso 1		
	03. Área Bruta de Construção	108,75
	05.2. Área Exterior Coberta (varandas)	22,30
		131,06 m²
Piso 2		
	03. Área Bruta de Construção	40,81
		40,81 m²
		303,81 m²

Quadro de Áreas Casa 2		
Piso	Designação	Área
Piso 0		
	03. Área Bruta de Construção	120,38
	05.1. Área Exterior Coberta (terraços)	12,73
		133,11 m²
Piso 1		
	03. Área Bruta de Construção	108,75
	05.2. Área Exterior Coberta (varandas)	22,30
		131,05 m²
Piso 2		
	03. Área Bruta de Construção	40,81
		40,81 m²
		304,97 m²

QUADROS SINÓTICOS - Áreas Úteis

Quadro de Áreas Casa 1		
Piso	Designação	Área
Piso 0		
	Arrumos	2,71
	Cozinha	19,67
	Escritório	16,00
	Garagem	22,19
	Hall	16,44
	Lavandaria	6,00
	Logradouro	77,30
Piso 2	WC Escritório	6,37
	WC Serviço	2,86
		169,54 m²


Quadro de Áreas Casa 2		
Piso	Designação	Área
Piso 0		
	Arrumos	2,71
	Cozinha	19,67
	Escritório	16,00
	Garagem	24,45
	Hall	16,44
	Lavandaria	6,69
	Logradouro	75,79
Piso 2	WC Escritório	6,37
	WC Serviço	2,86
		170,98 m²

Quadro de Áreas Casa 1		
Piso	Designação	Área
Piso 1		
	Circulação	18,49
	Quarto Suite 1	18,68
	Quarto Suite 2	12,94
	Quarto Suite 3	19,06
	Varanda Frente	3,56
	Varanda Lateral	3,46
	Varanda Traseiras	4,13
Piso 2	WC Suite 1	5,34
	WC Suite 2	5,48
	WC Suite 3	5,43
		96,57 m²

Quadro de Áreas Casa 2		
Piso	Designação	Área
Piso 1		
	Circulação	18,49
	Quarto Suite 1	18,68
	Quarto Suite 2	12,94
	Quarto Suite 3	19,07
	Varanda Frente	3,56
	Varanda Lateral	3,46
	Varanda Traseiras	4,13
Piso 2	WC Suite 1	5,34
	WC Suite 2	5,48
	WC Suite 3	5,41
		96,56 m²

QUADROS SINÓTICOS - Parâmetros Urbanísticos

Descrição	Área m2
01. Área Total do Prédio Existente	548,58
02. Área de Implantação Proposta	300,27
02.1 Área de Implantação Existente	84,12
02.2 Área de Implantação Existente (anexos)	142,29
03. Área Bruta de Construção	538,72
04. Área de Estacionamento	97,55
05. Área de Impermeabilização	24,09
05.1. Área Exterior Coberta (terraços)	14,73
05.2. Área Exterior Coberta (varandas)	25,31
06. Área Verde	115,86
07. Área de Piscina	36,12
08. Área Exterior Pavimentada	84,45
09. Área Útil	413,64
10. Área Habitável	252,98

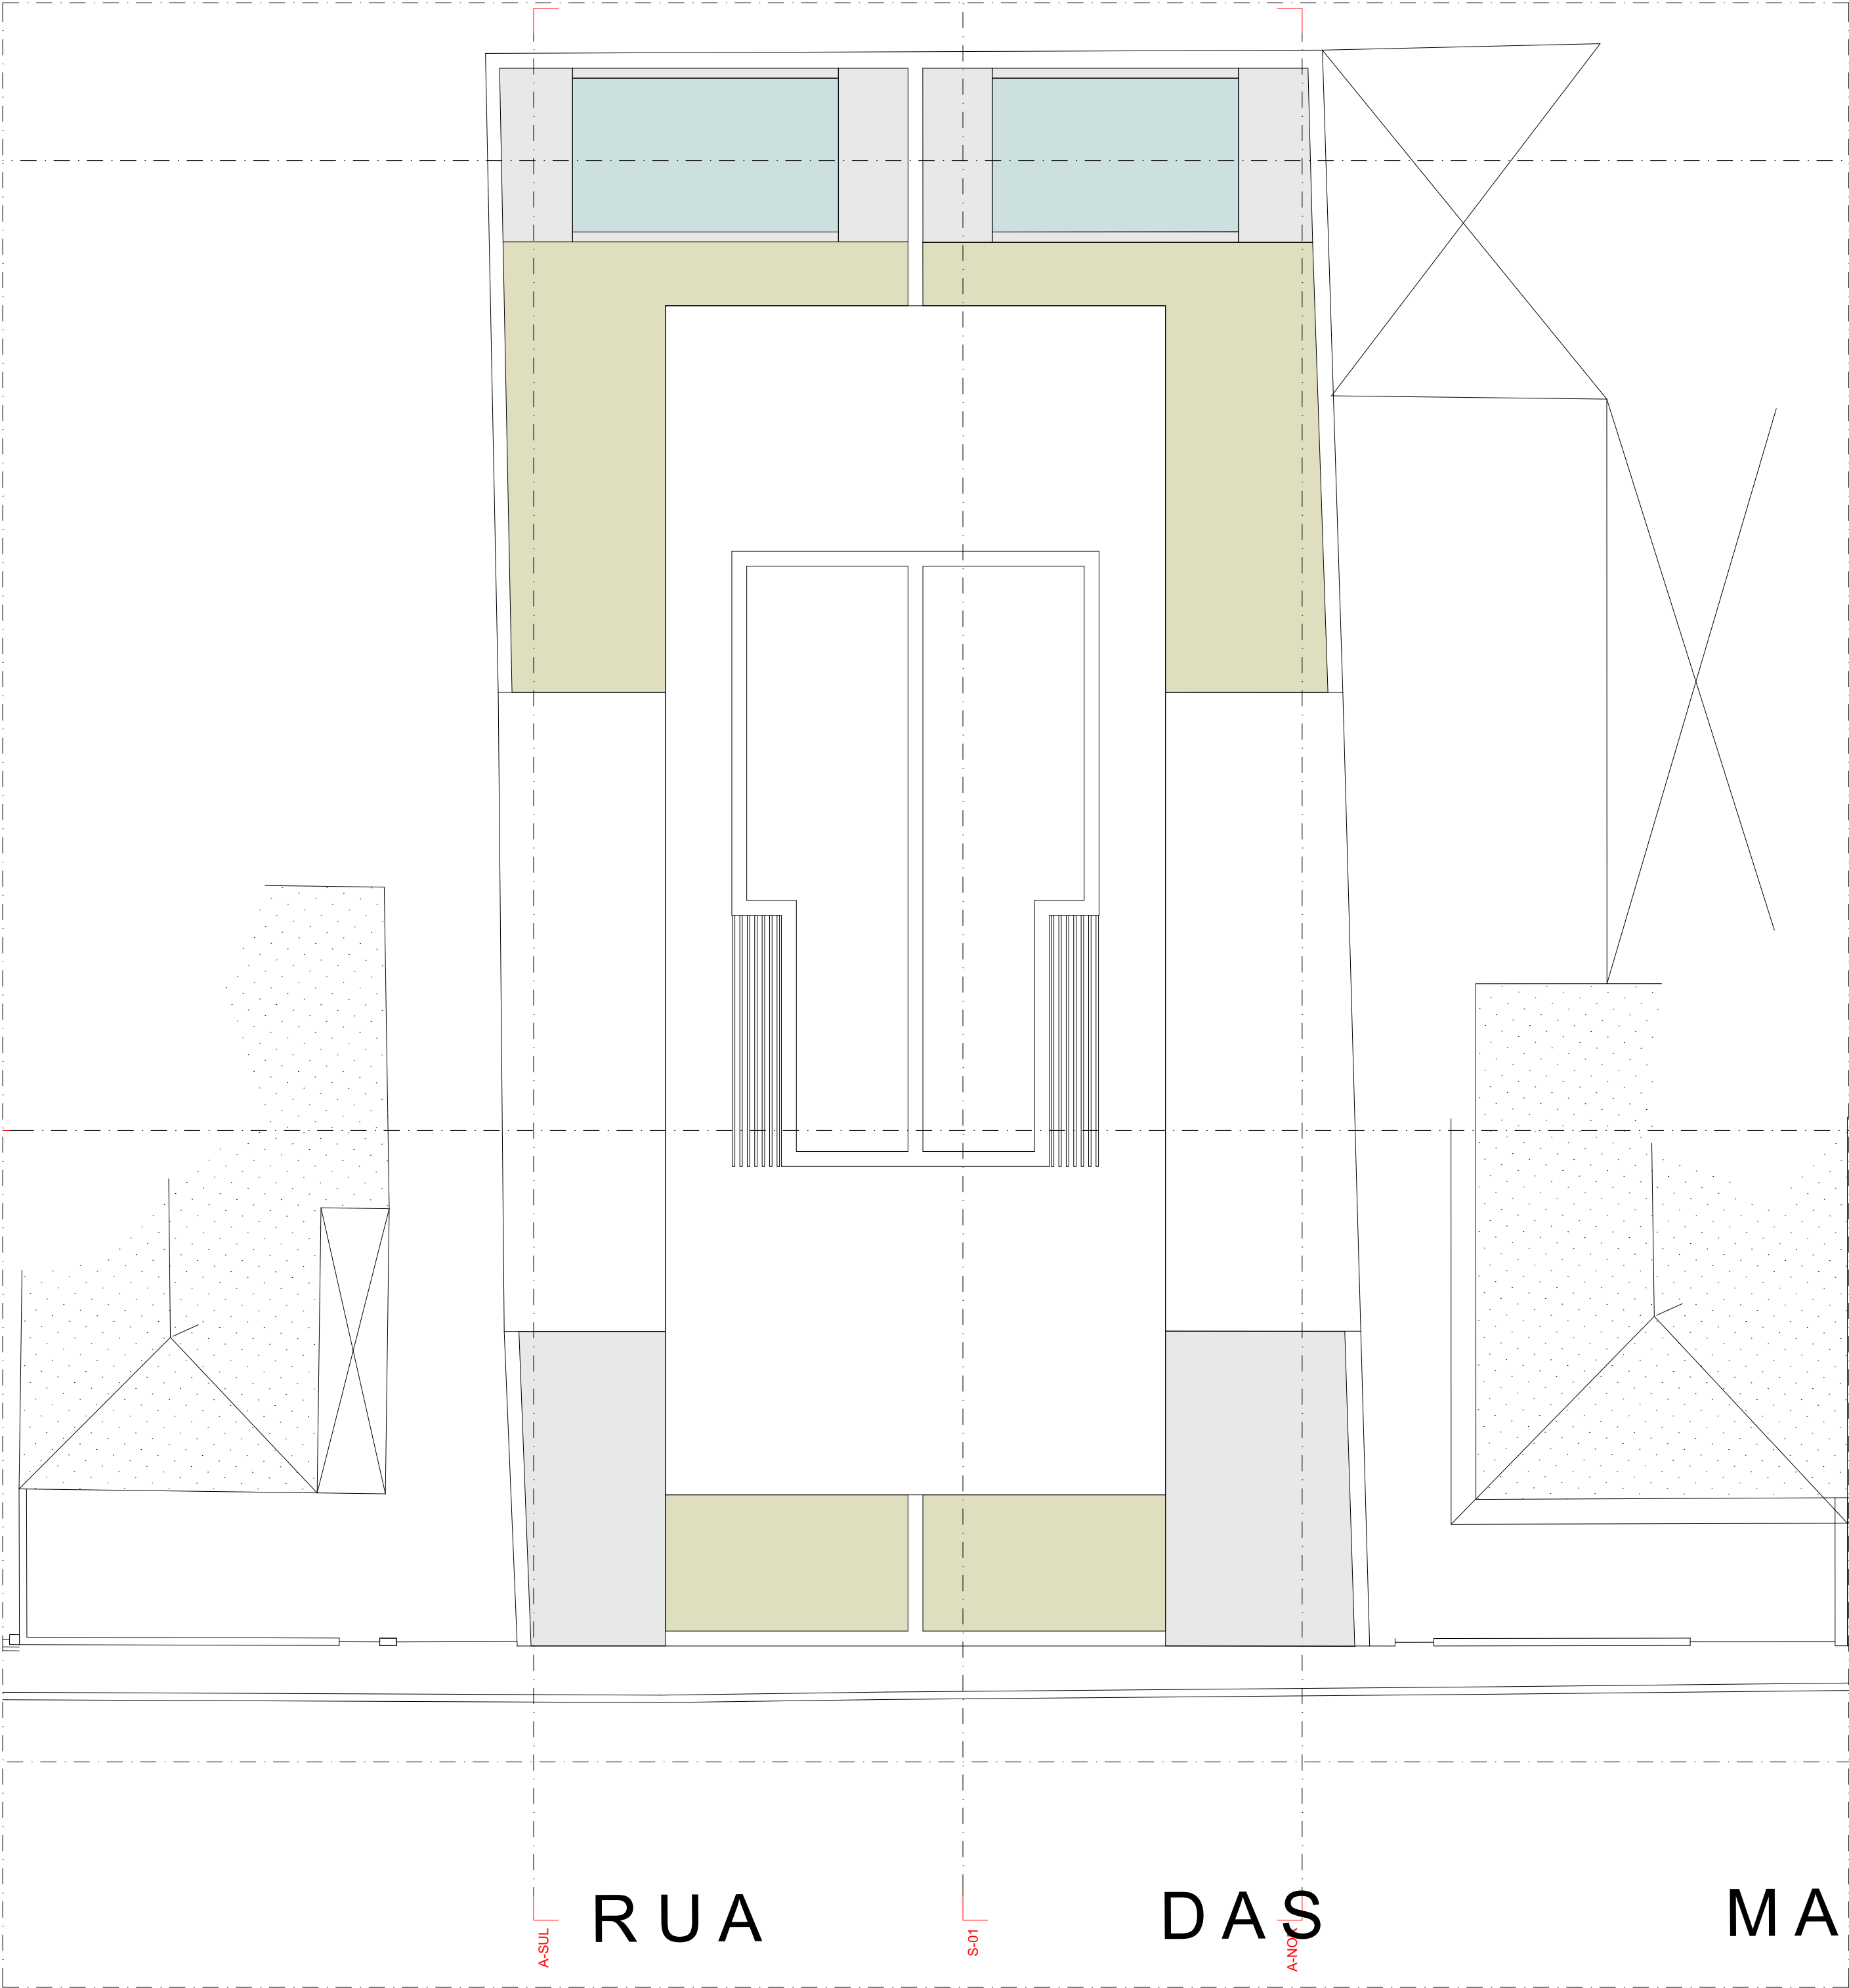

QUADROS SINÓTICOS - Áreas Brutas

Quadro de Áreas Casa 1		
Piso	Designação	Área
Piso 0		
	03. Área Bruta de Construção	119,21
	05.1. Área Exterior Coberta (terraços)	12,73
		131,94 m²
Piso 1		
	03. Área Bruta de Construção	108,75
	05.2. Área Exterior Coberta (varandas)	22,30
		131,06 m²
Piso 2		
	03. Área Bruta de Construção	40,81
		40,81 m²
		303,81 m²

Quadro de Áreas Casa 2		
Piso	Designação	Área
Piso 0		
	03. Área Bruta de Construção	120,38
	05.1. Área Exterior Coberta (terraços)	12,73
		133,11 m²
Piso 1		
	03. Área Bruta de Construção	108,75
	05.2. Área Exterior Coberta (varandas)	22,30
		131,05 m²
Piso 2		
	03. Área Bruta de Construção	40,81
		40,81 m²
		304,97 m²

QUADROS SINÓTICOS - Áreas Úteis

Quadro de Áreas Casa 1		
Piso	Designação	Área
Piso 0		
	Árremos	2,71
	Cozinha	19,67
	Escritório	16,00
	Garagem	22,19
	Hall	16,44
	Lavandaria	6,00
	Logradouro	77,30
	WC Escritório	6,37
	WC Serviço	2,86
		169,54 m²

Quadro de Áreas Casa 2		
Piso	Designação	Área
Piso 0		
	Árremos	2,71
	Cozinha	19,67
	Escritório	16,00
	Garagem	24,45
	Hall	16,44
	Lavandaria	6,69
	Logradouro	75,79
	WC Escritório	6,37
	WC Serviço	2,86
		170,98 m²

Quadro de Áreas Casa 2		
Piso	Designação	Área
Piso 1		
	Circulação	18,49
	Quarto Suite 1	18,68
	Quarto Suite 2	12,94
	Quarto Suite 3	19,06
	Varanda Frente	3,56
	Varanda Lateral	3,46
	Varanda Traseiras	4,13
	WC Suite 1	5,34
	WC Suite 2	5,48
	WC Suite 3	5,43
		96,57 m²

Quadro de Áreas Casa 2		
Piso	Designação	Área
Piso 2		
	Sala	22,57
		22,57 m²
		288,68 m²


Quadro de Áreas Casa 2		
Piso	Designação	Área
Piso 0		
	Árremos	2,71
	Cozinha	19,67
	Escritório	16,00
	Garagem	24,45
	Hall	16,44
	Lavandaria	6,69
	Logradouro	75,79
	WC Escritório	6,37
	WC Serviço	2,86
		170,98 m²

Quadro de Áreas Casa 2		
Piso	Designação	Área
Piso 1		
	Circulação	18,49
	Quarto Suite 1	18,68
	Quarto Suite 2	12,94
	Quarto Suite 3	19,07
	Varanda Frente	3,56
	Varanda Lateral	3,46
	Varanda Traseiras	4,13
	WC Suite 1	5,34
	WC Suite 2	5,48
	WC Suite 3	5,41
		96,56 m²


Quadro de Áreas Casa 2		
Piso	Designação	Área
Piso 2		
	Sala	22,57
		22,57 m²
		290,11 m²

QUADROS SINÓTICOS - Parâmetros Urbanísticos


Descrição	Área m2
01. Área Total do Prédio Existente	548,58
02. Área de Implantação Proposta	300,27
02.1 Área de Implantação Existente	84,12
02.2 Área de Implantação Existente (anexos)	142,29
03. Área Bruta de Construção	538,72
04. Área de Estacionamento	97,55
05. Área de Impermeabilização	24,09
05.1. Área Exterior Coberta (terraços)	14,73
05.2. Área Exterior Coberta (varandas)	25,31
06. Área Verde	115,86
07. Área de Piscina	36,12
08. Área Exterior Pavimentada	84,45
09. Área Útil	413,64
10. Área Habitável	252,98

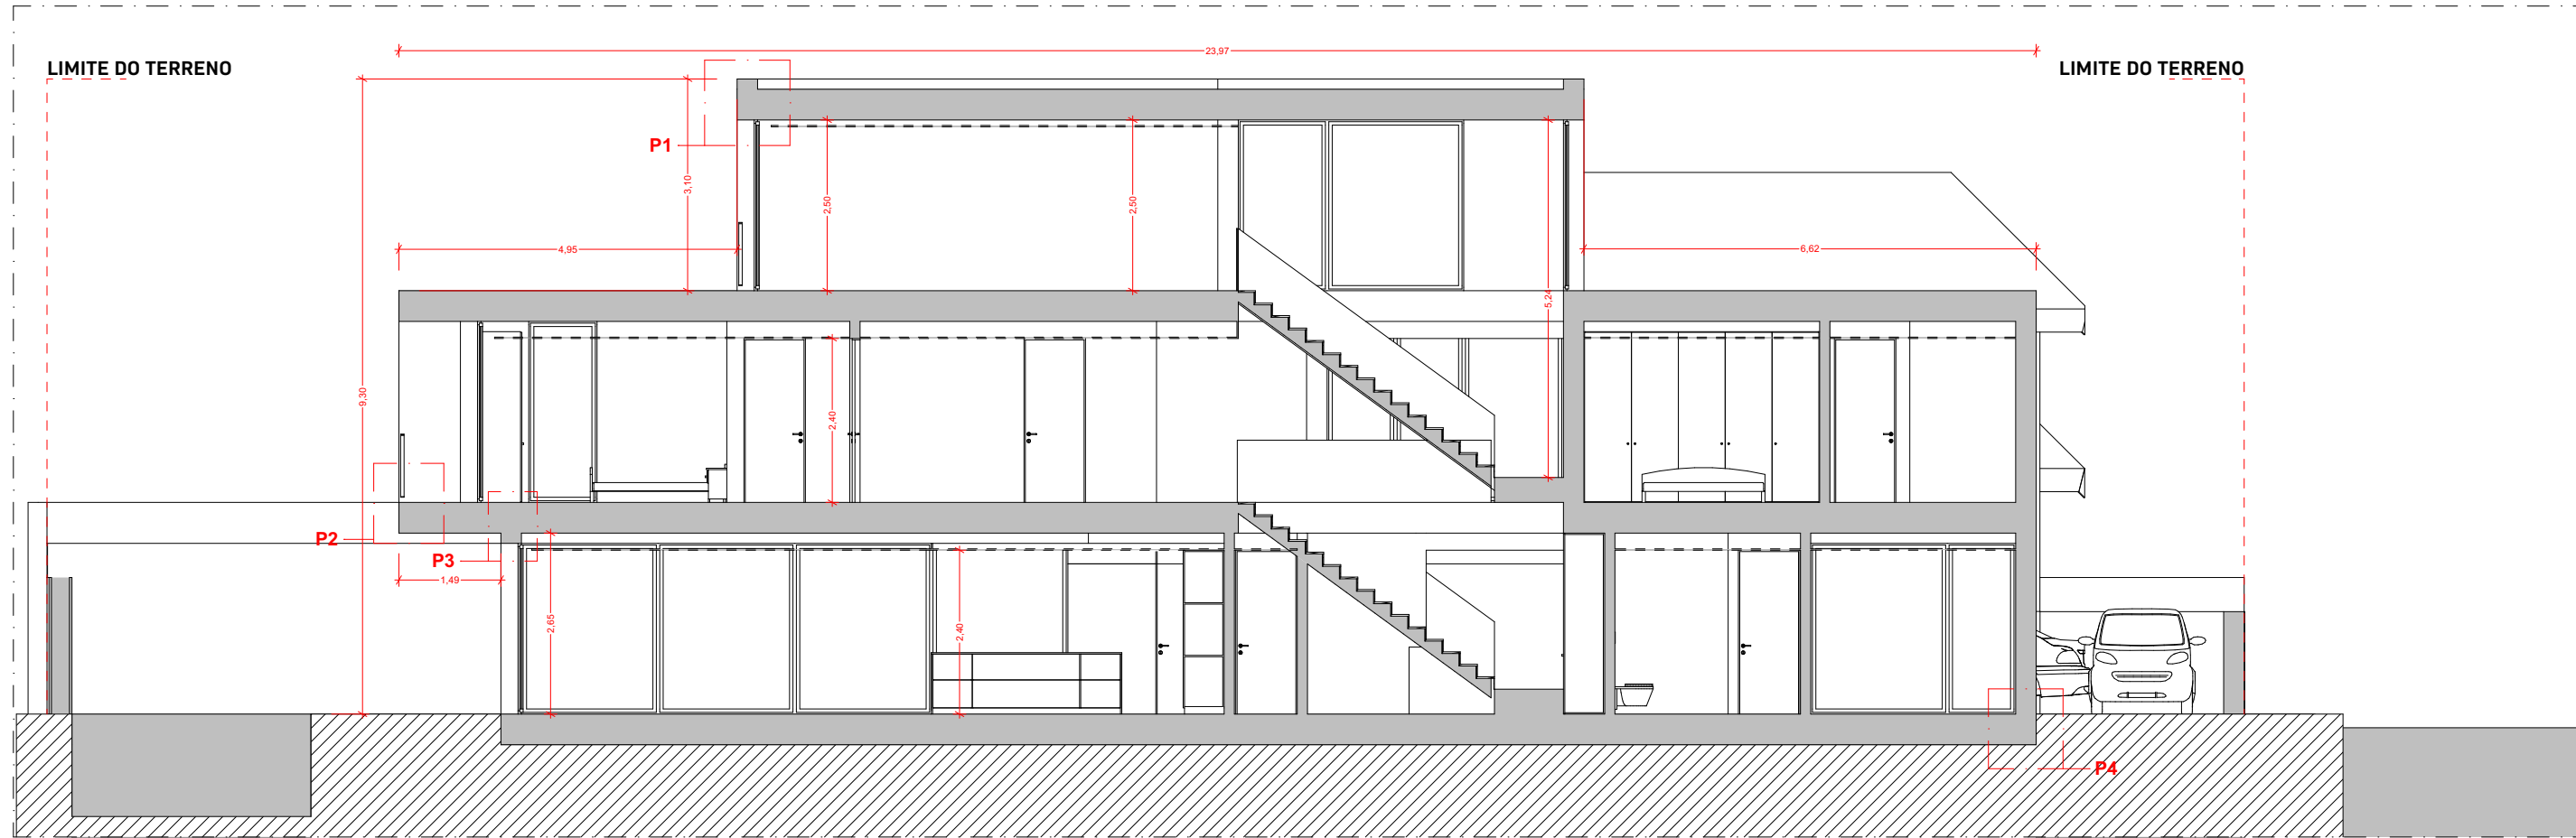

S-01 - CORTE

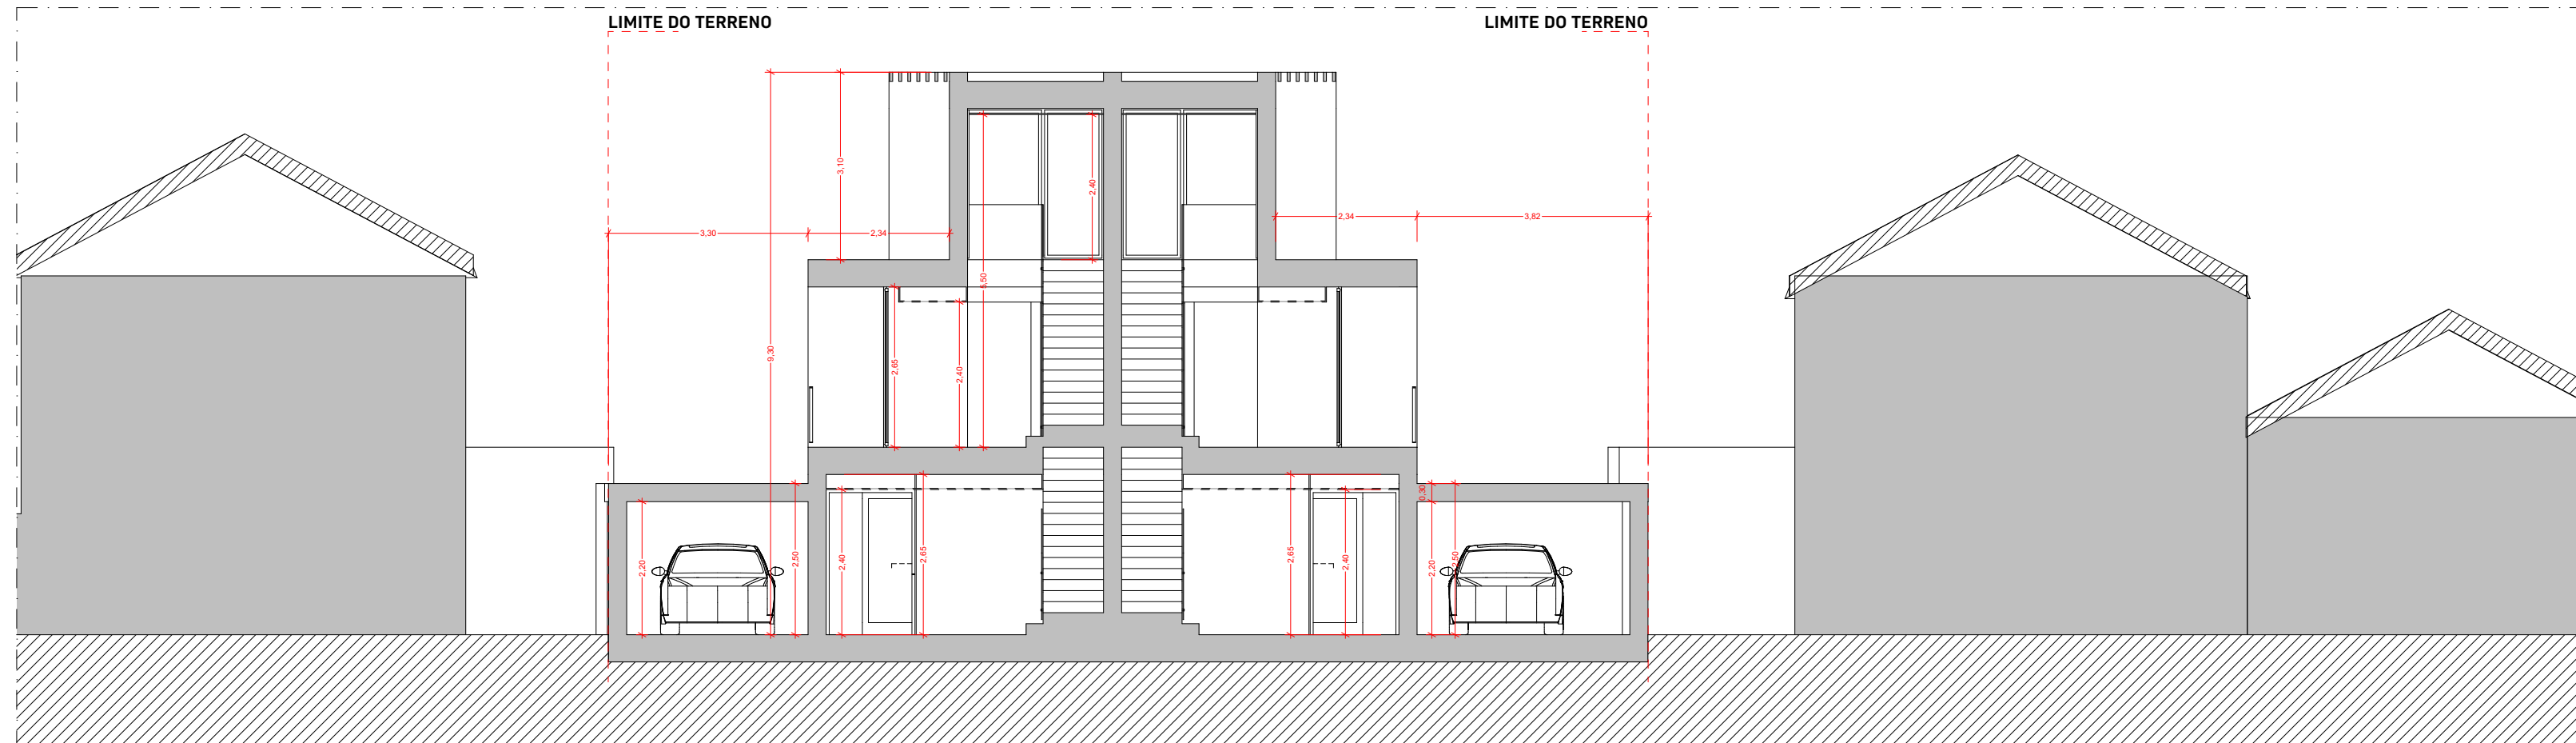


S-02 - CORTE

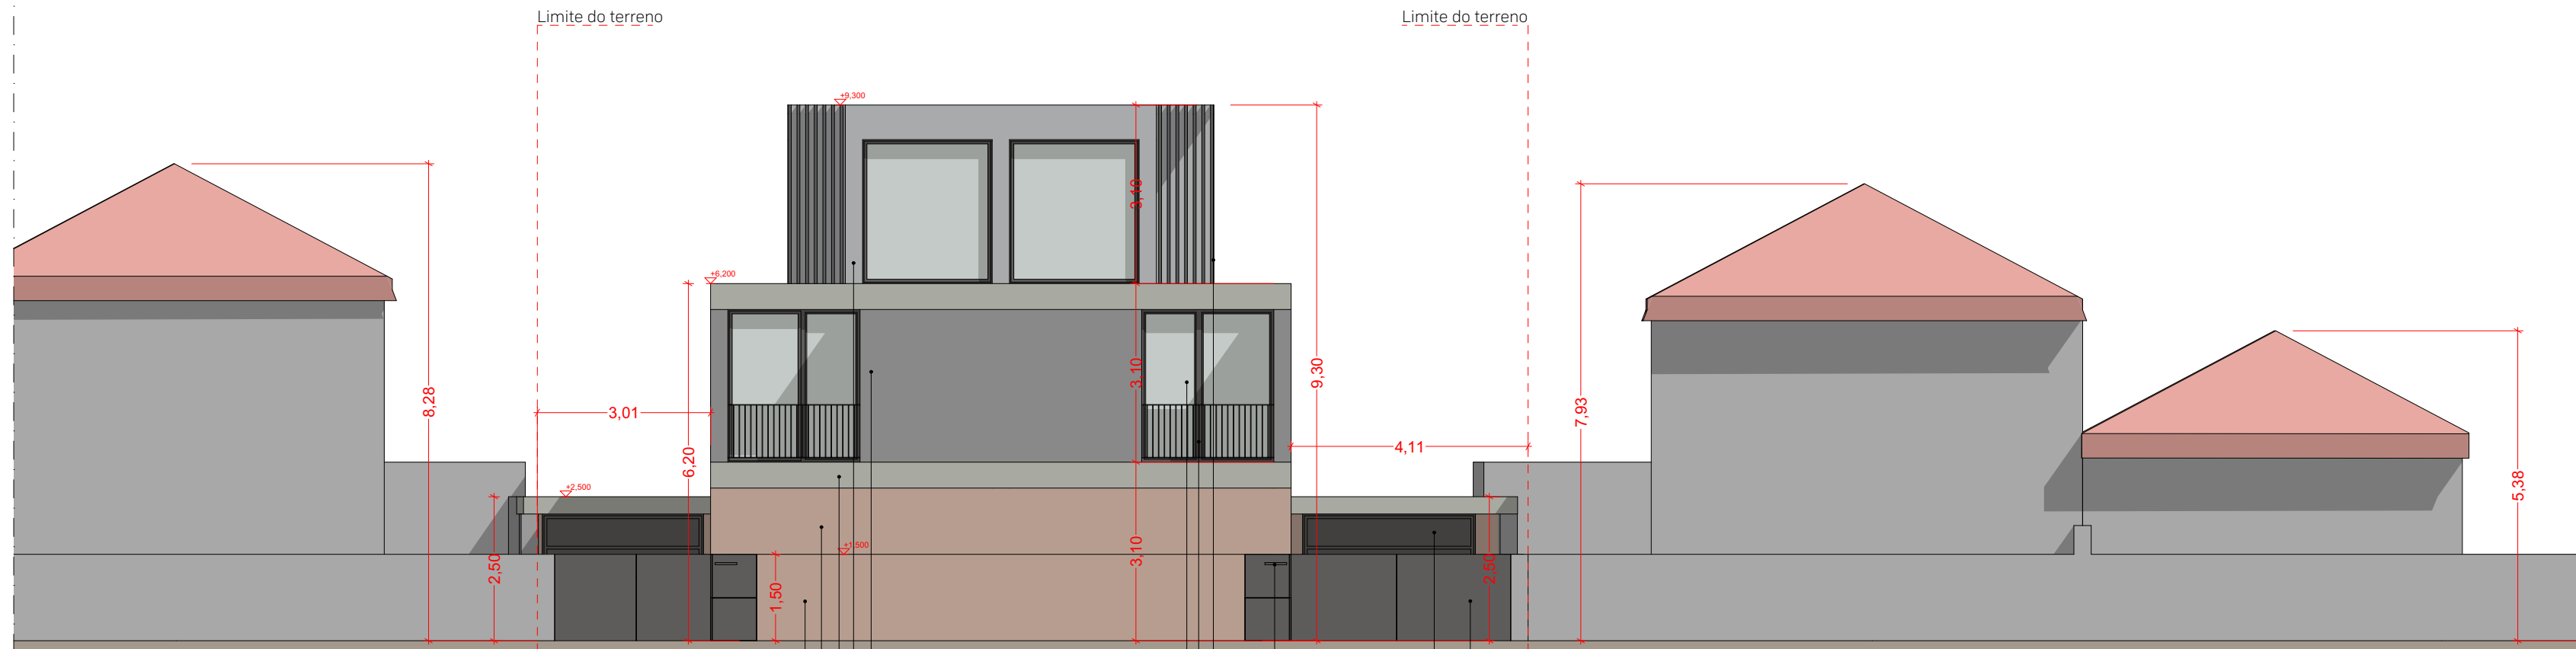


A-POE - ALÇADO POENTE




A-NAS - ALÇADO NASCENTE

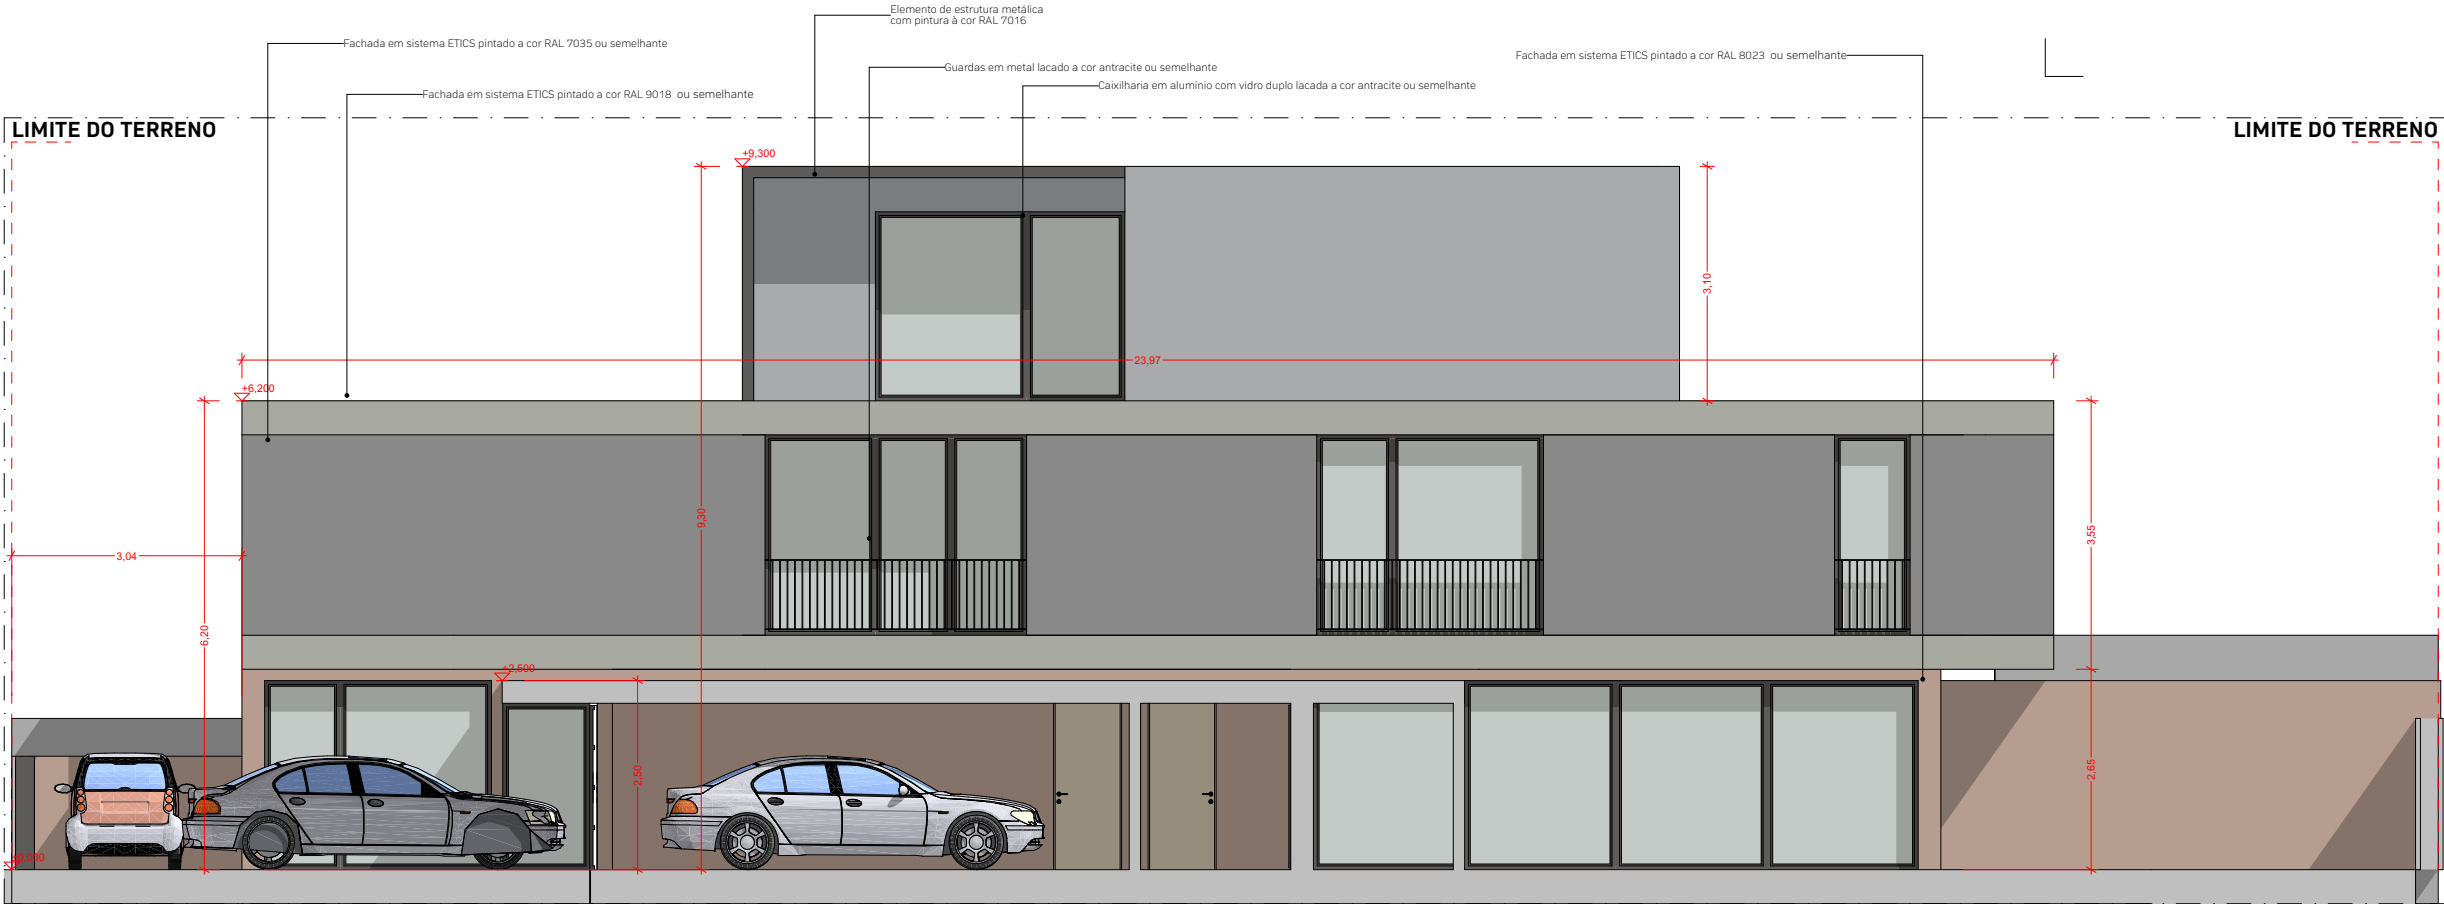

A-NOR - ALÇADO NORTE

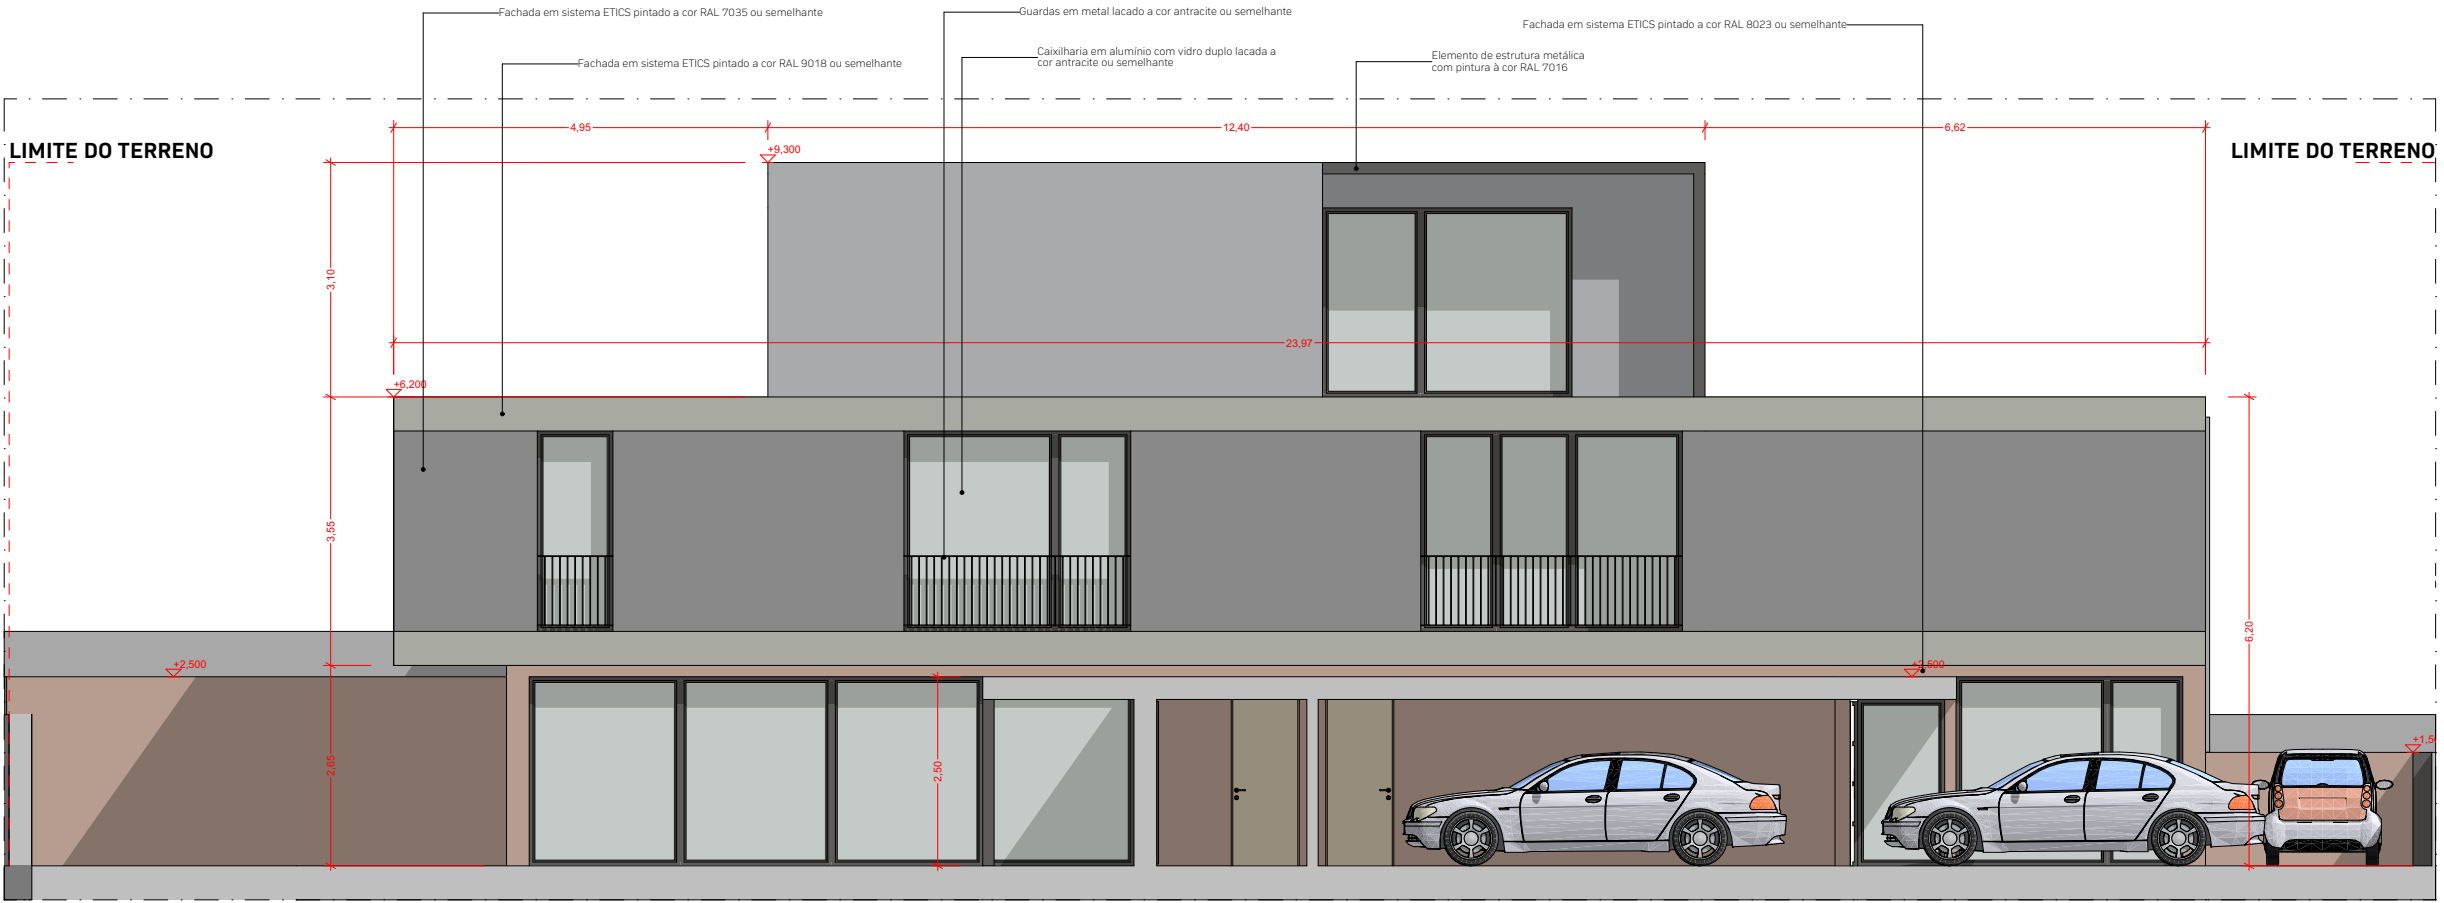

A-SUL - ALÇADO SUL

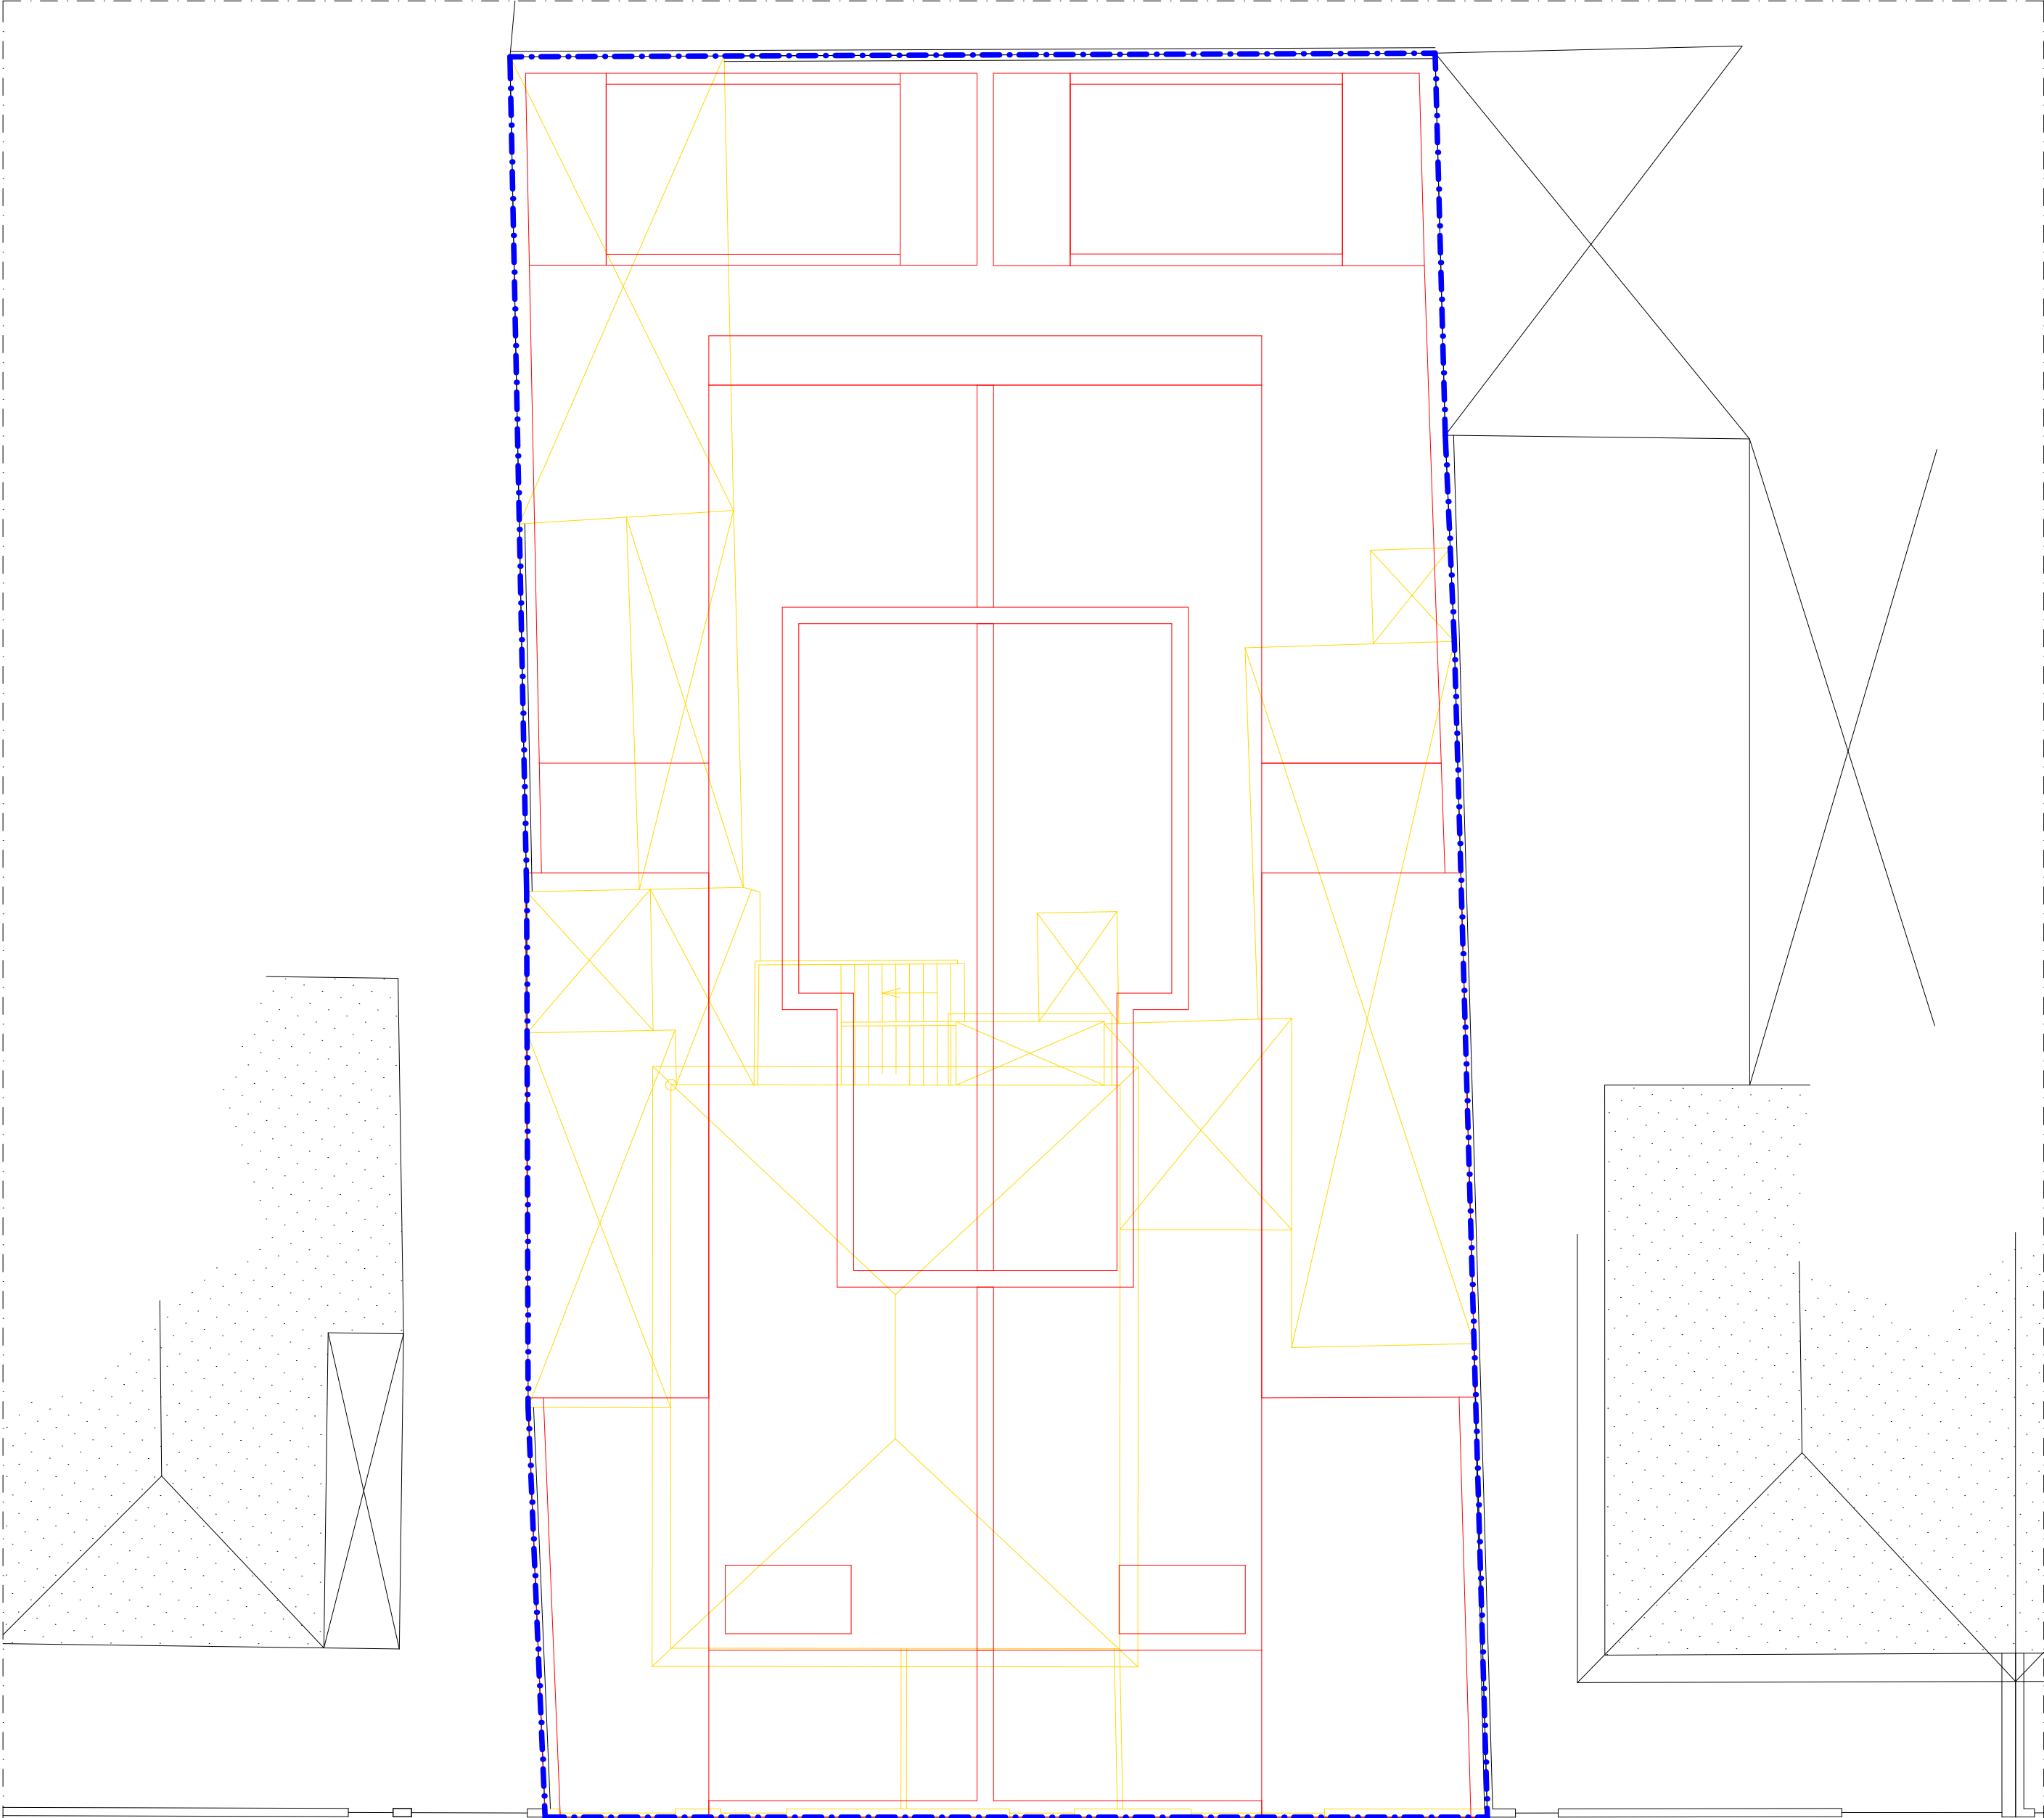

LEGENDA

- Limites do prédio
- Elementos existentes / a manter
- Elementos a construir
- Elementos a demolir

Quadro de Áreas Geral	
Descrição	Área m2
01. Área Total do Prédio Existente	548,58
02. Área de Implantação Proposta	300,27
02.1 Área de Implantação Existente	84,12
02.2 Área de Implantação Existente (anexos)	142,29
03. Área Bruta de Construção	538,72
04. Área de Estacionamento	97,55
05. Área de Impermeabilização	24,09
05.1. Área Exterior Coberta (terraços)	14,73
05.2. Área Exterior Coberta (varandas)	25,31
06. Área Verde	115,86
07. Área de Piscina	36,12
08. Área Exterior Pavimentada	84,45
09. Área Útil	413,64
10. Área Habitável	252,98

